


GLOBAL COLLEGE OF TECHNOLOGY

MID-BANESHOWR, KATHMANDU



LINE WORK ARCHITECTS

Kaldhara, Kathmandu
9851172835, 9851172838

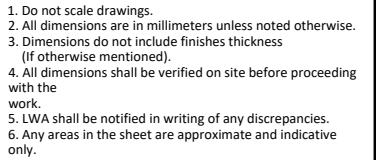

CLIENT: GLOBAL COLLEGE
OF TECHNOLOGY

DATE: _____

SCALE:

DRAWN BY : Ar. Dikshant Man Baisyet


DESIGN BY : Ar. Sabin Maharjan

SHEET No.:A-01

PAGE No.: 01



MASTERPLAN

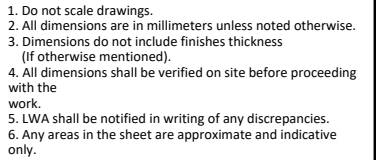[illegible]

CLIENT: GLOBAL COLLEGE
OF TECHNOLOGY

CLIENT:

ARCHITECTURAL DRAWING
(MAIN BLOCK)

DATE: _____


SCALE: _____

DRAWN BY : Ar. Dikshant Man Baisyet


DESIGN BY : Ar. Sabin Maharjan

SHEET No.: A-02

PAGE No.: 02

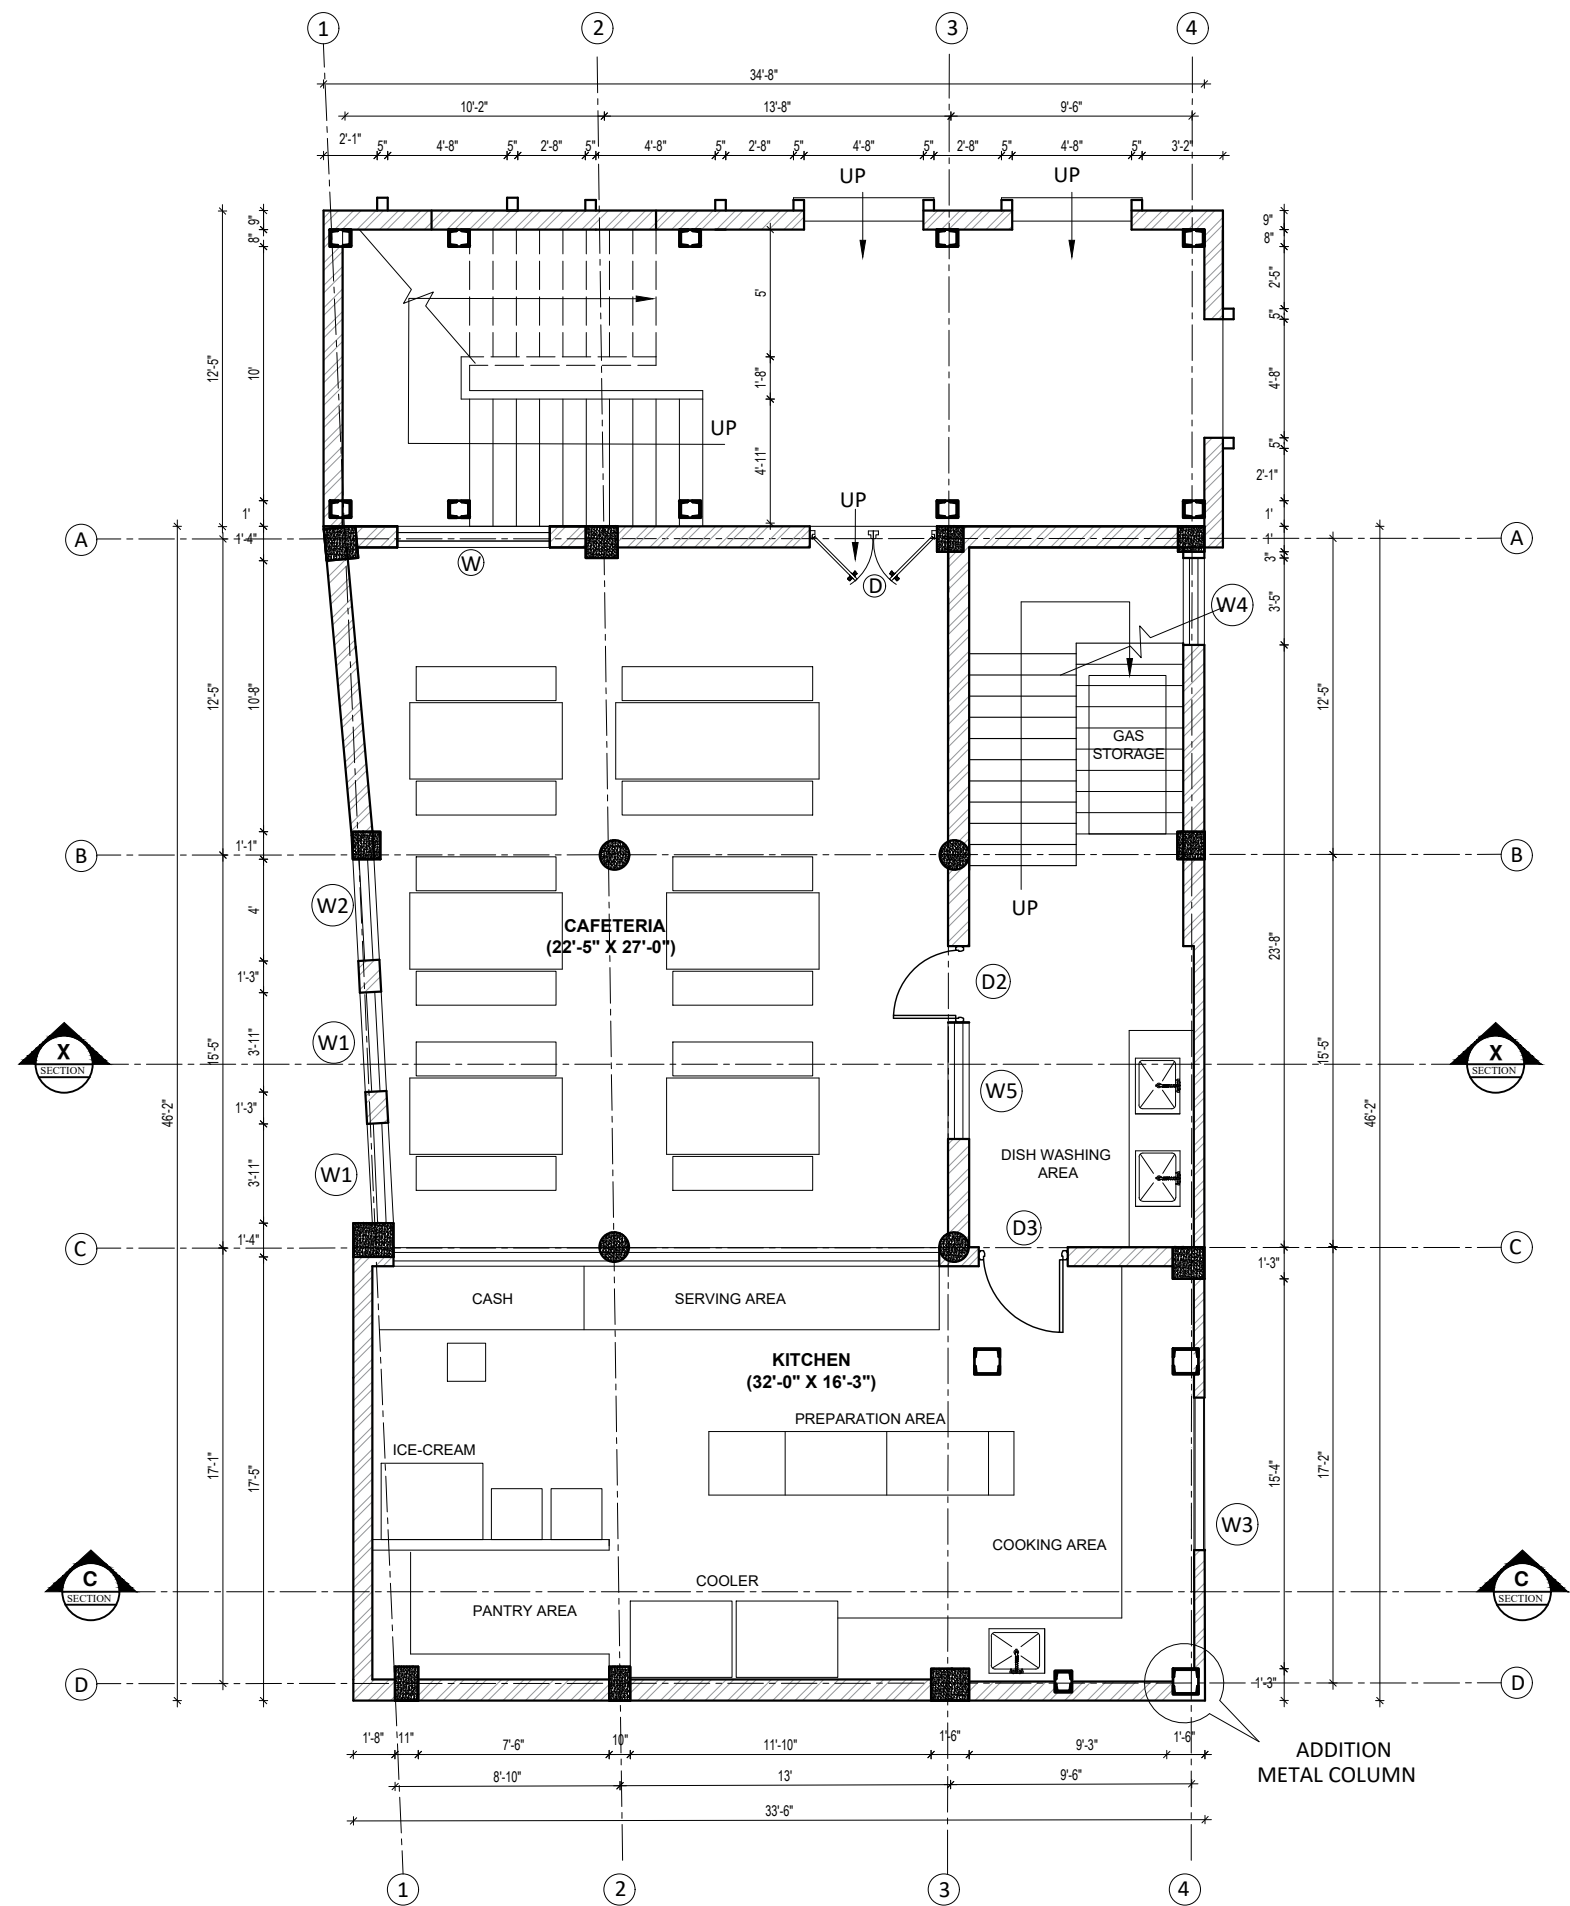

GROUND FLOOR PLAN
AREA: 1988.18 SQ. FT.

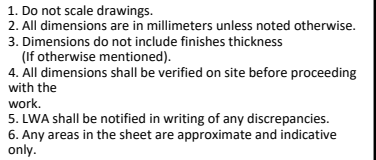[illegible]

CLIENT: GLOBAL COLLEGE
OF TECHNOLOGY

CLIENT:

ARCHITECTURAL DRAWING
(MAIN BLOCK)

DATE: _____


SCALE:

DRAWN BY : Ar. Dikshant Man Baisyet


DESIGN BY : Ar. Sabin Maharjan

SHEET No.: A-03

PAGE No.: 03

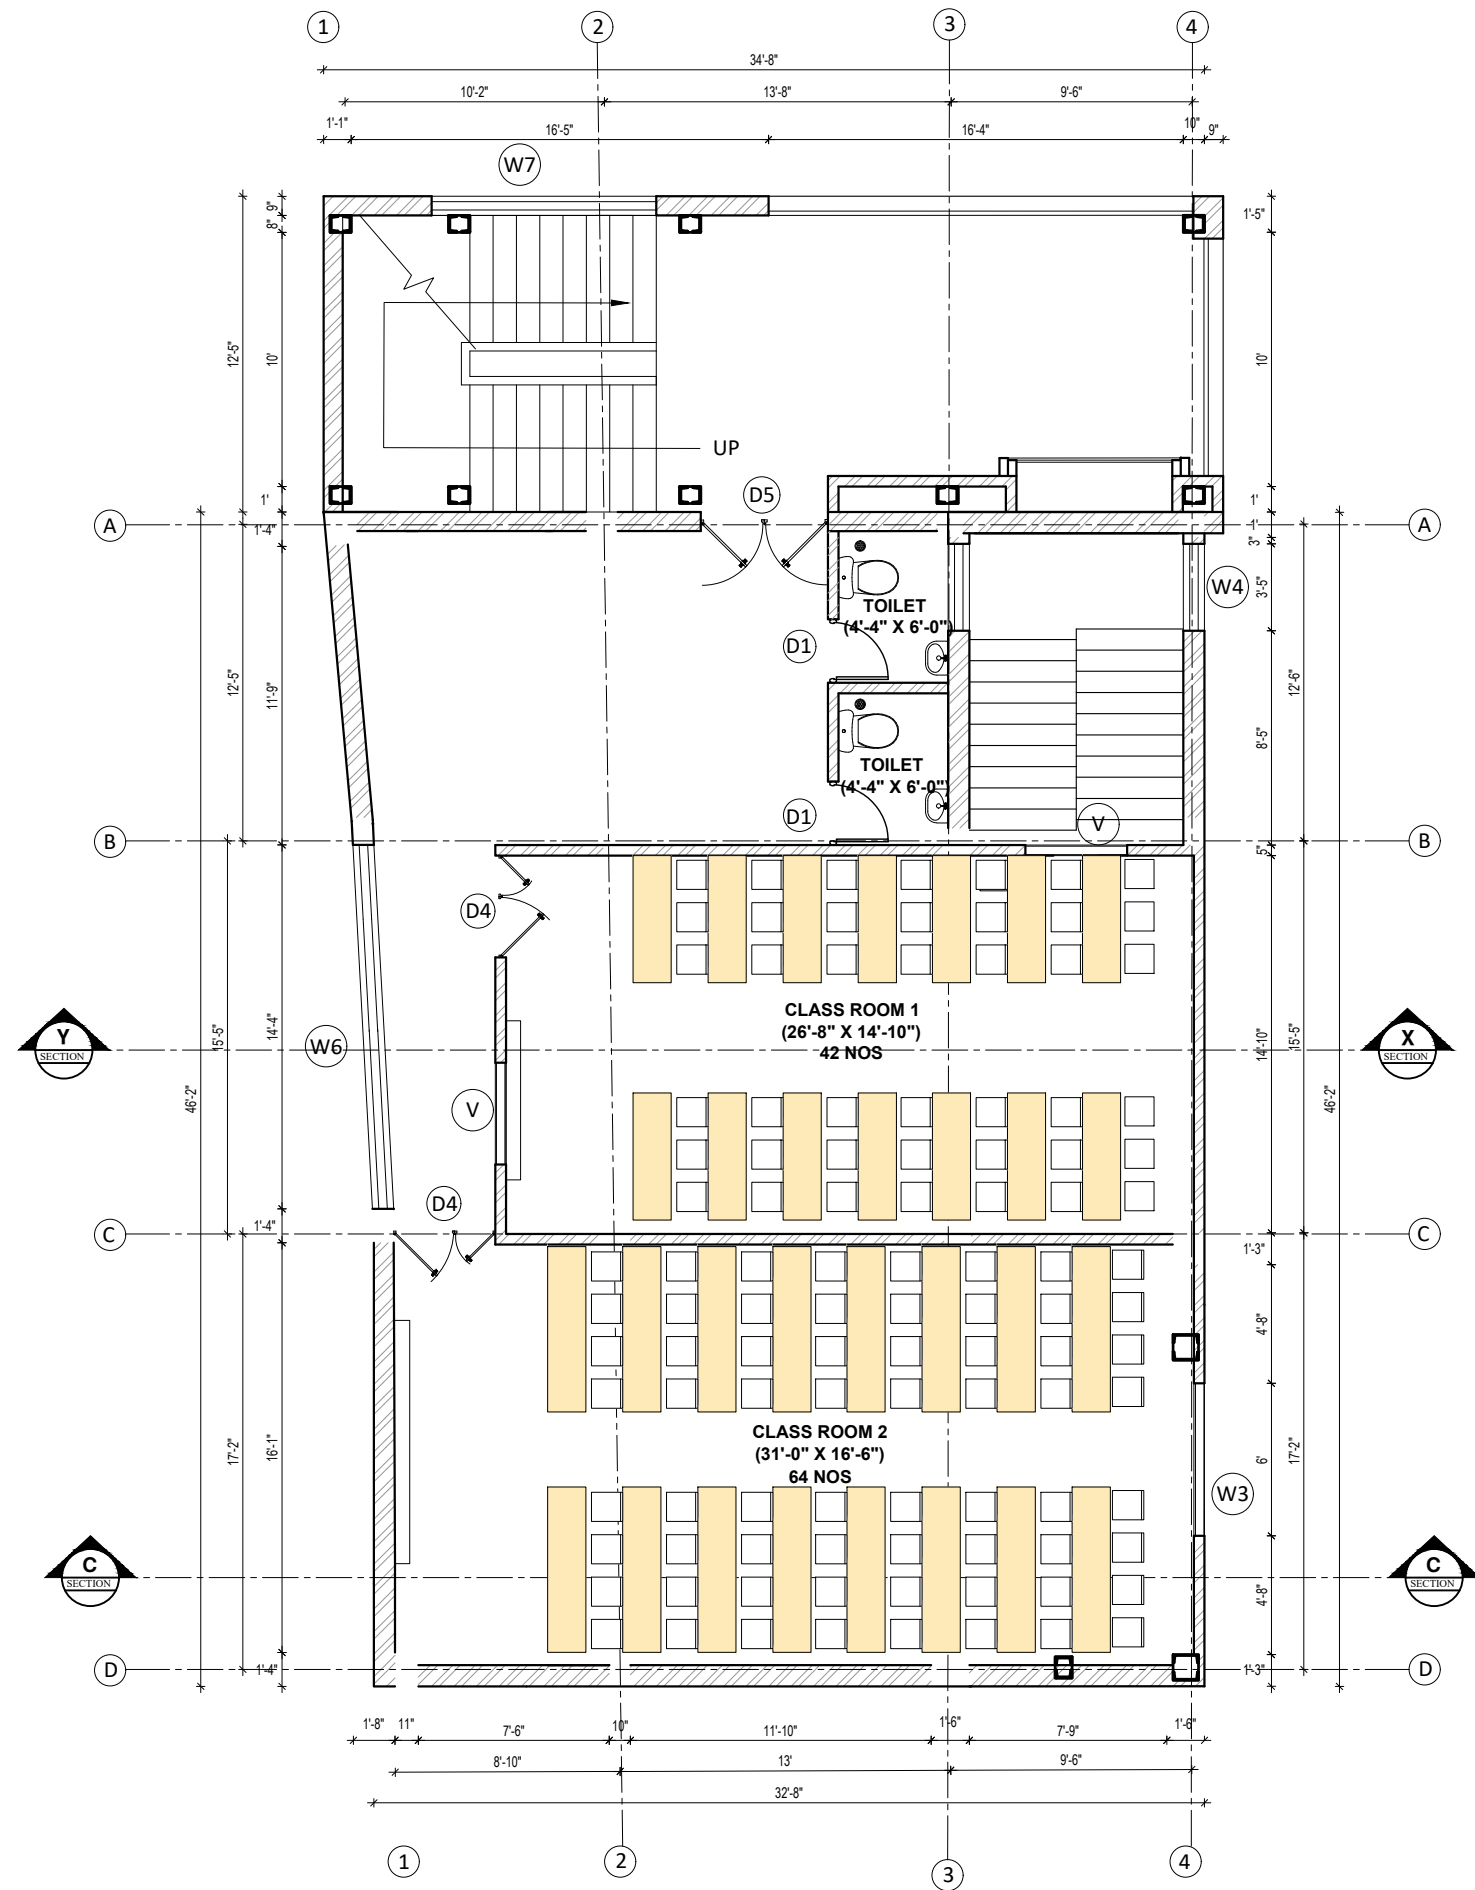

FIRST FLOOR PLAN
AREA: 1975.02 SQ. FT.

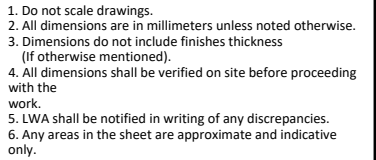[illegible]

CLIENT: GLOBAL COLLEGE
OF TECHNOLOGY

CLIENT:

ARCHITECTURAL DRAWING
(MAIN BLOCK)

DATE: _____


SCALE: _____

DRAWN BY : Ar. Dikshant Man Baisyet

DESIGN BY : Ar. Sabin Maharjan


SHEET No.: A-04

PAGE No.: 04

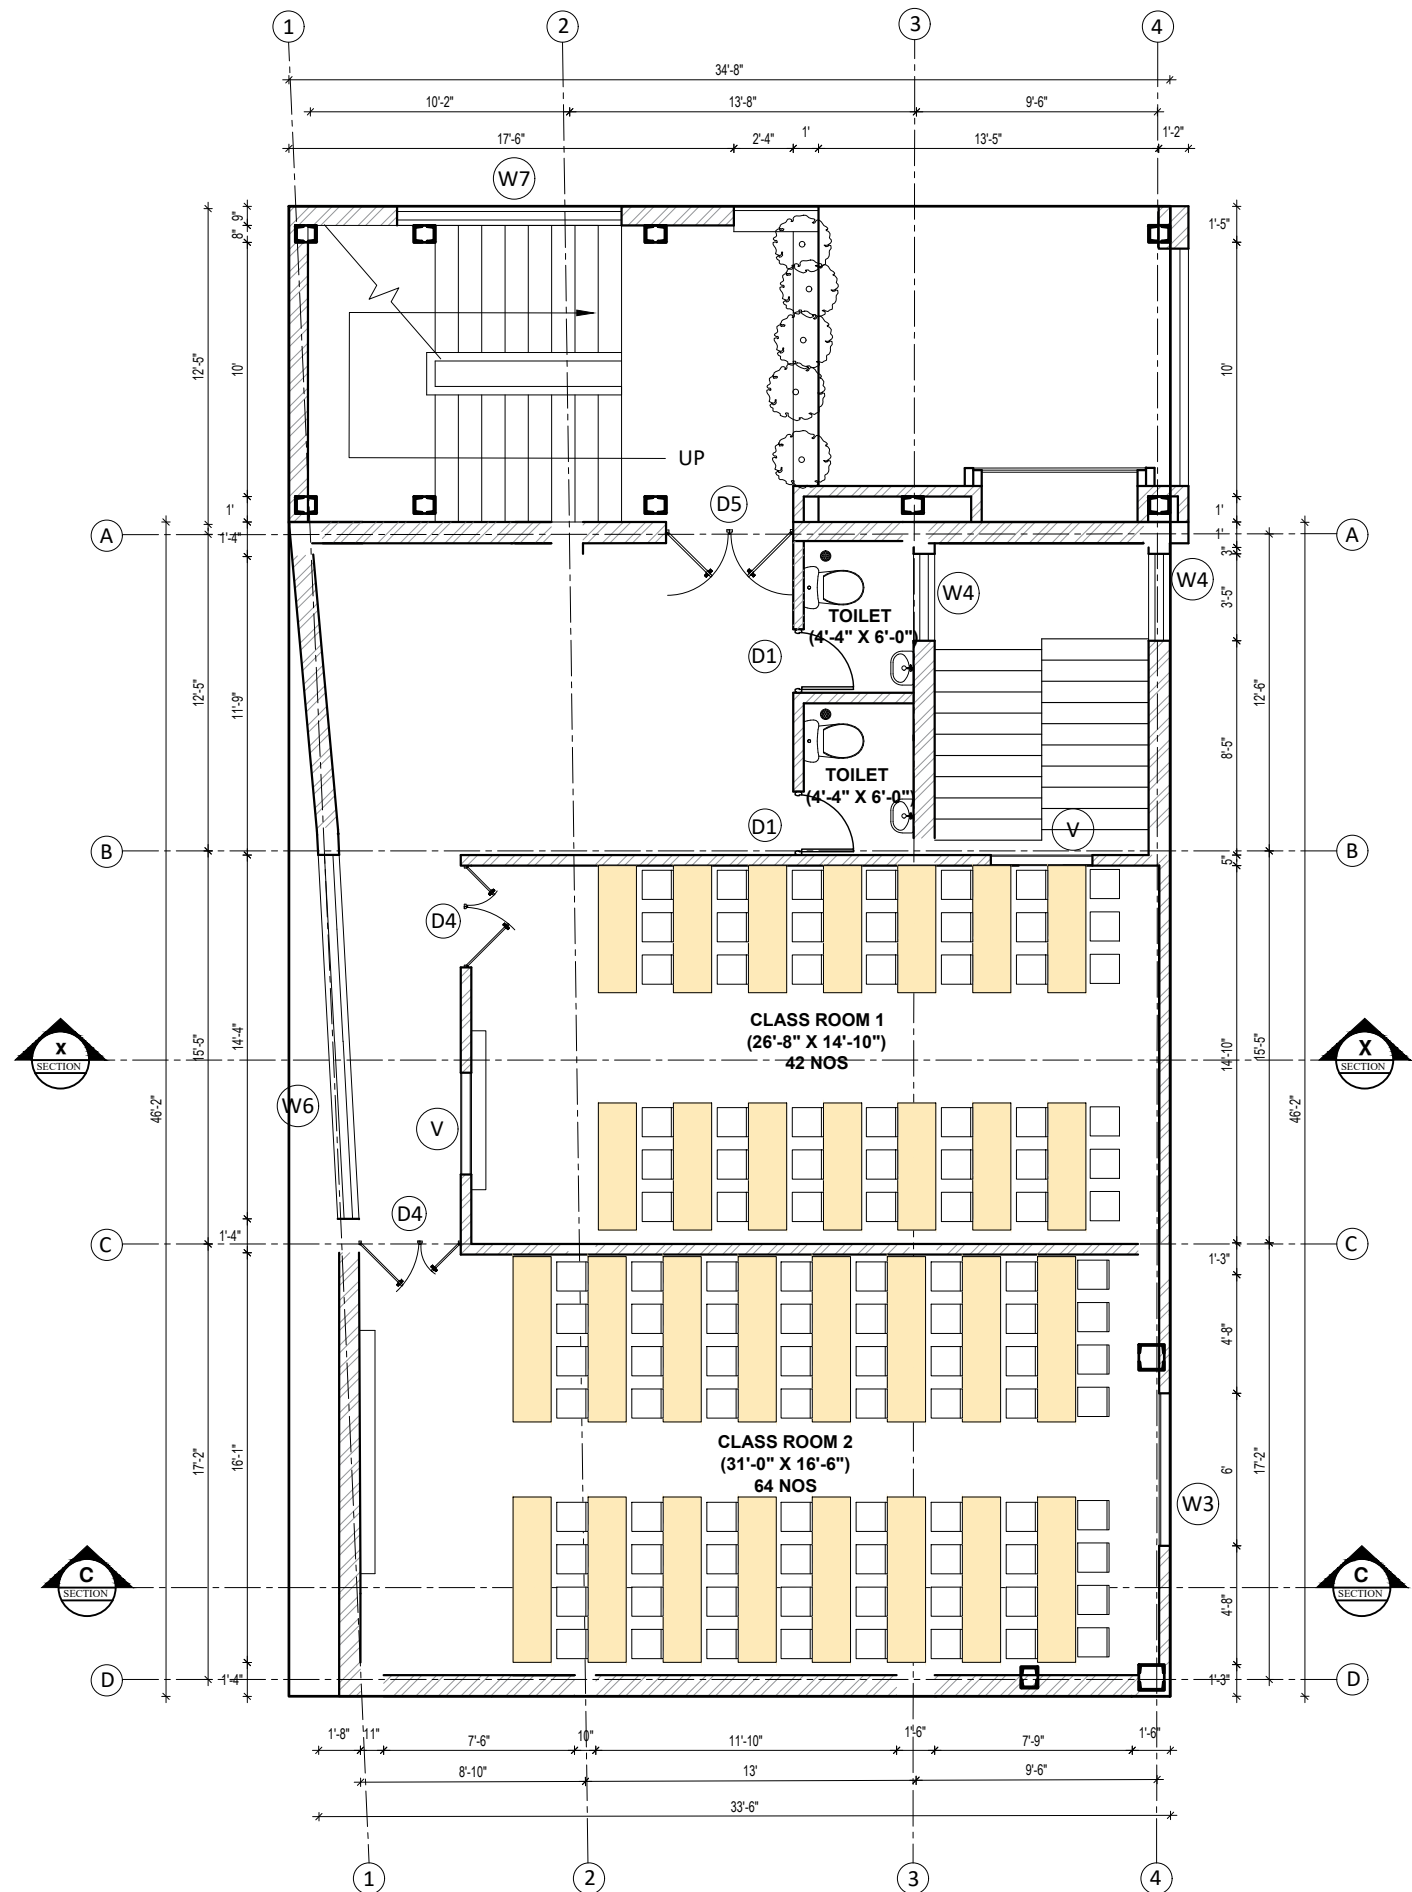

SECOND FLOOR PLAN

AREA: 1975.02 SQ. FT.

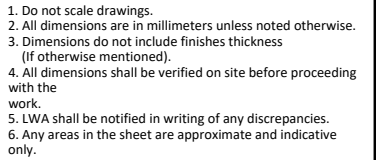[illegible]

CLIENT: GLOBAL COLLEGE
OF TECHNOLOGY

CLIENT:

ARCHITECTURAL DRAWING
(MAIN BLOCK)

DATE: _____


SCALE:

DRAWN BY : Ar. Dikshant Man Baisyet


DESIGN BY : Ar. Sabin Maharjan

SHEET No.: A-05


PAGE No.: 05

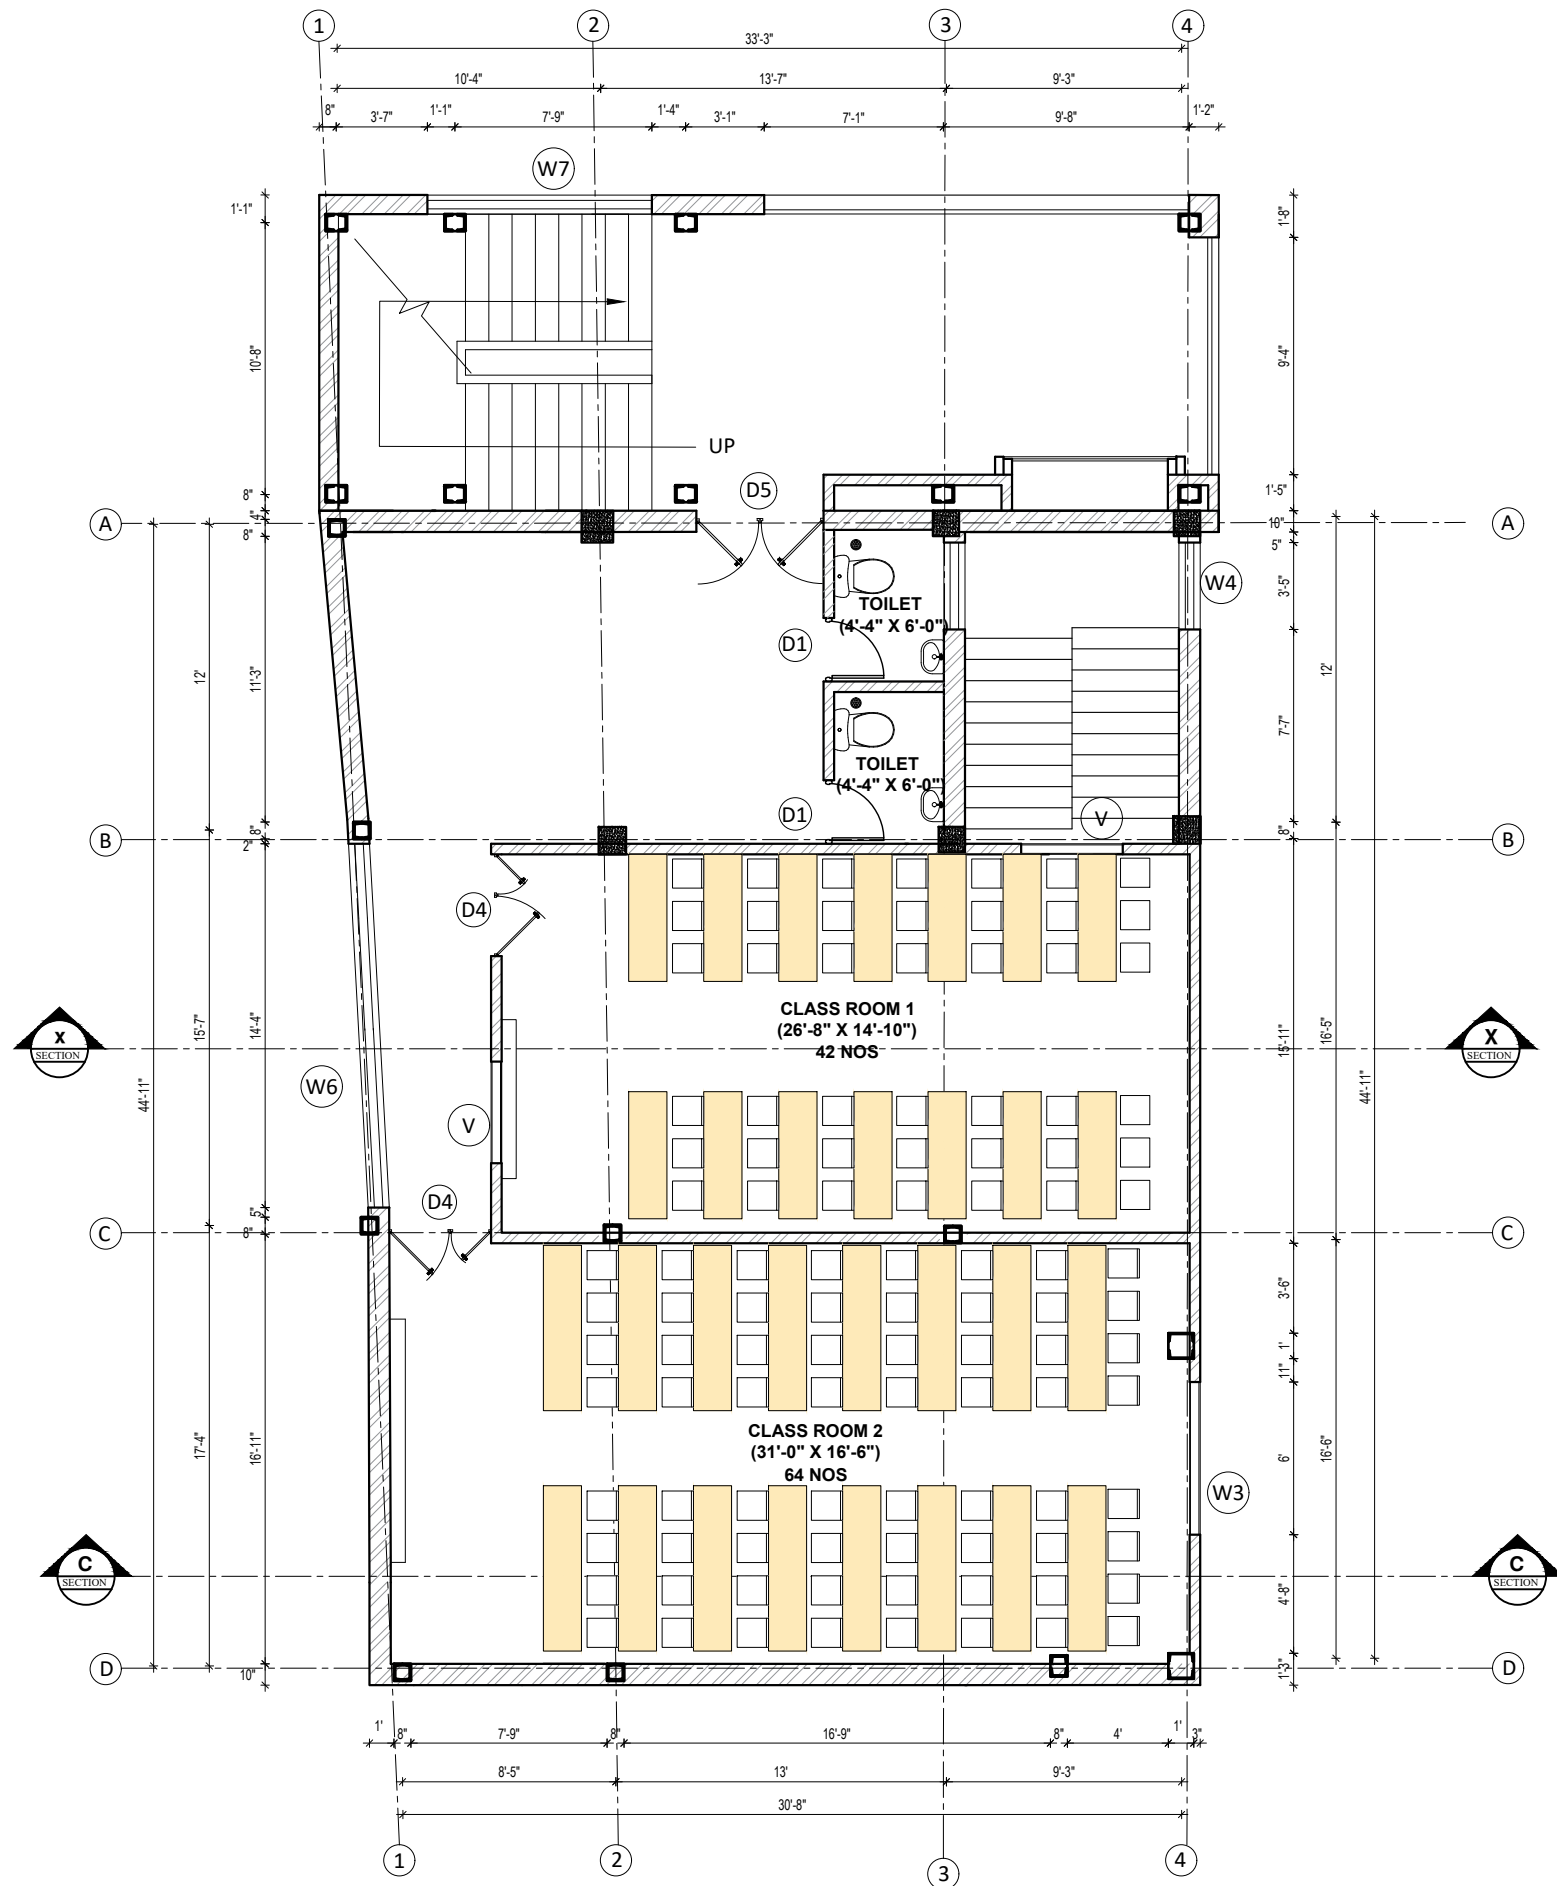

THIRD FLOOR PLAN
AREA: 1975.02 SQ. FT.

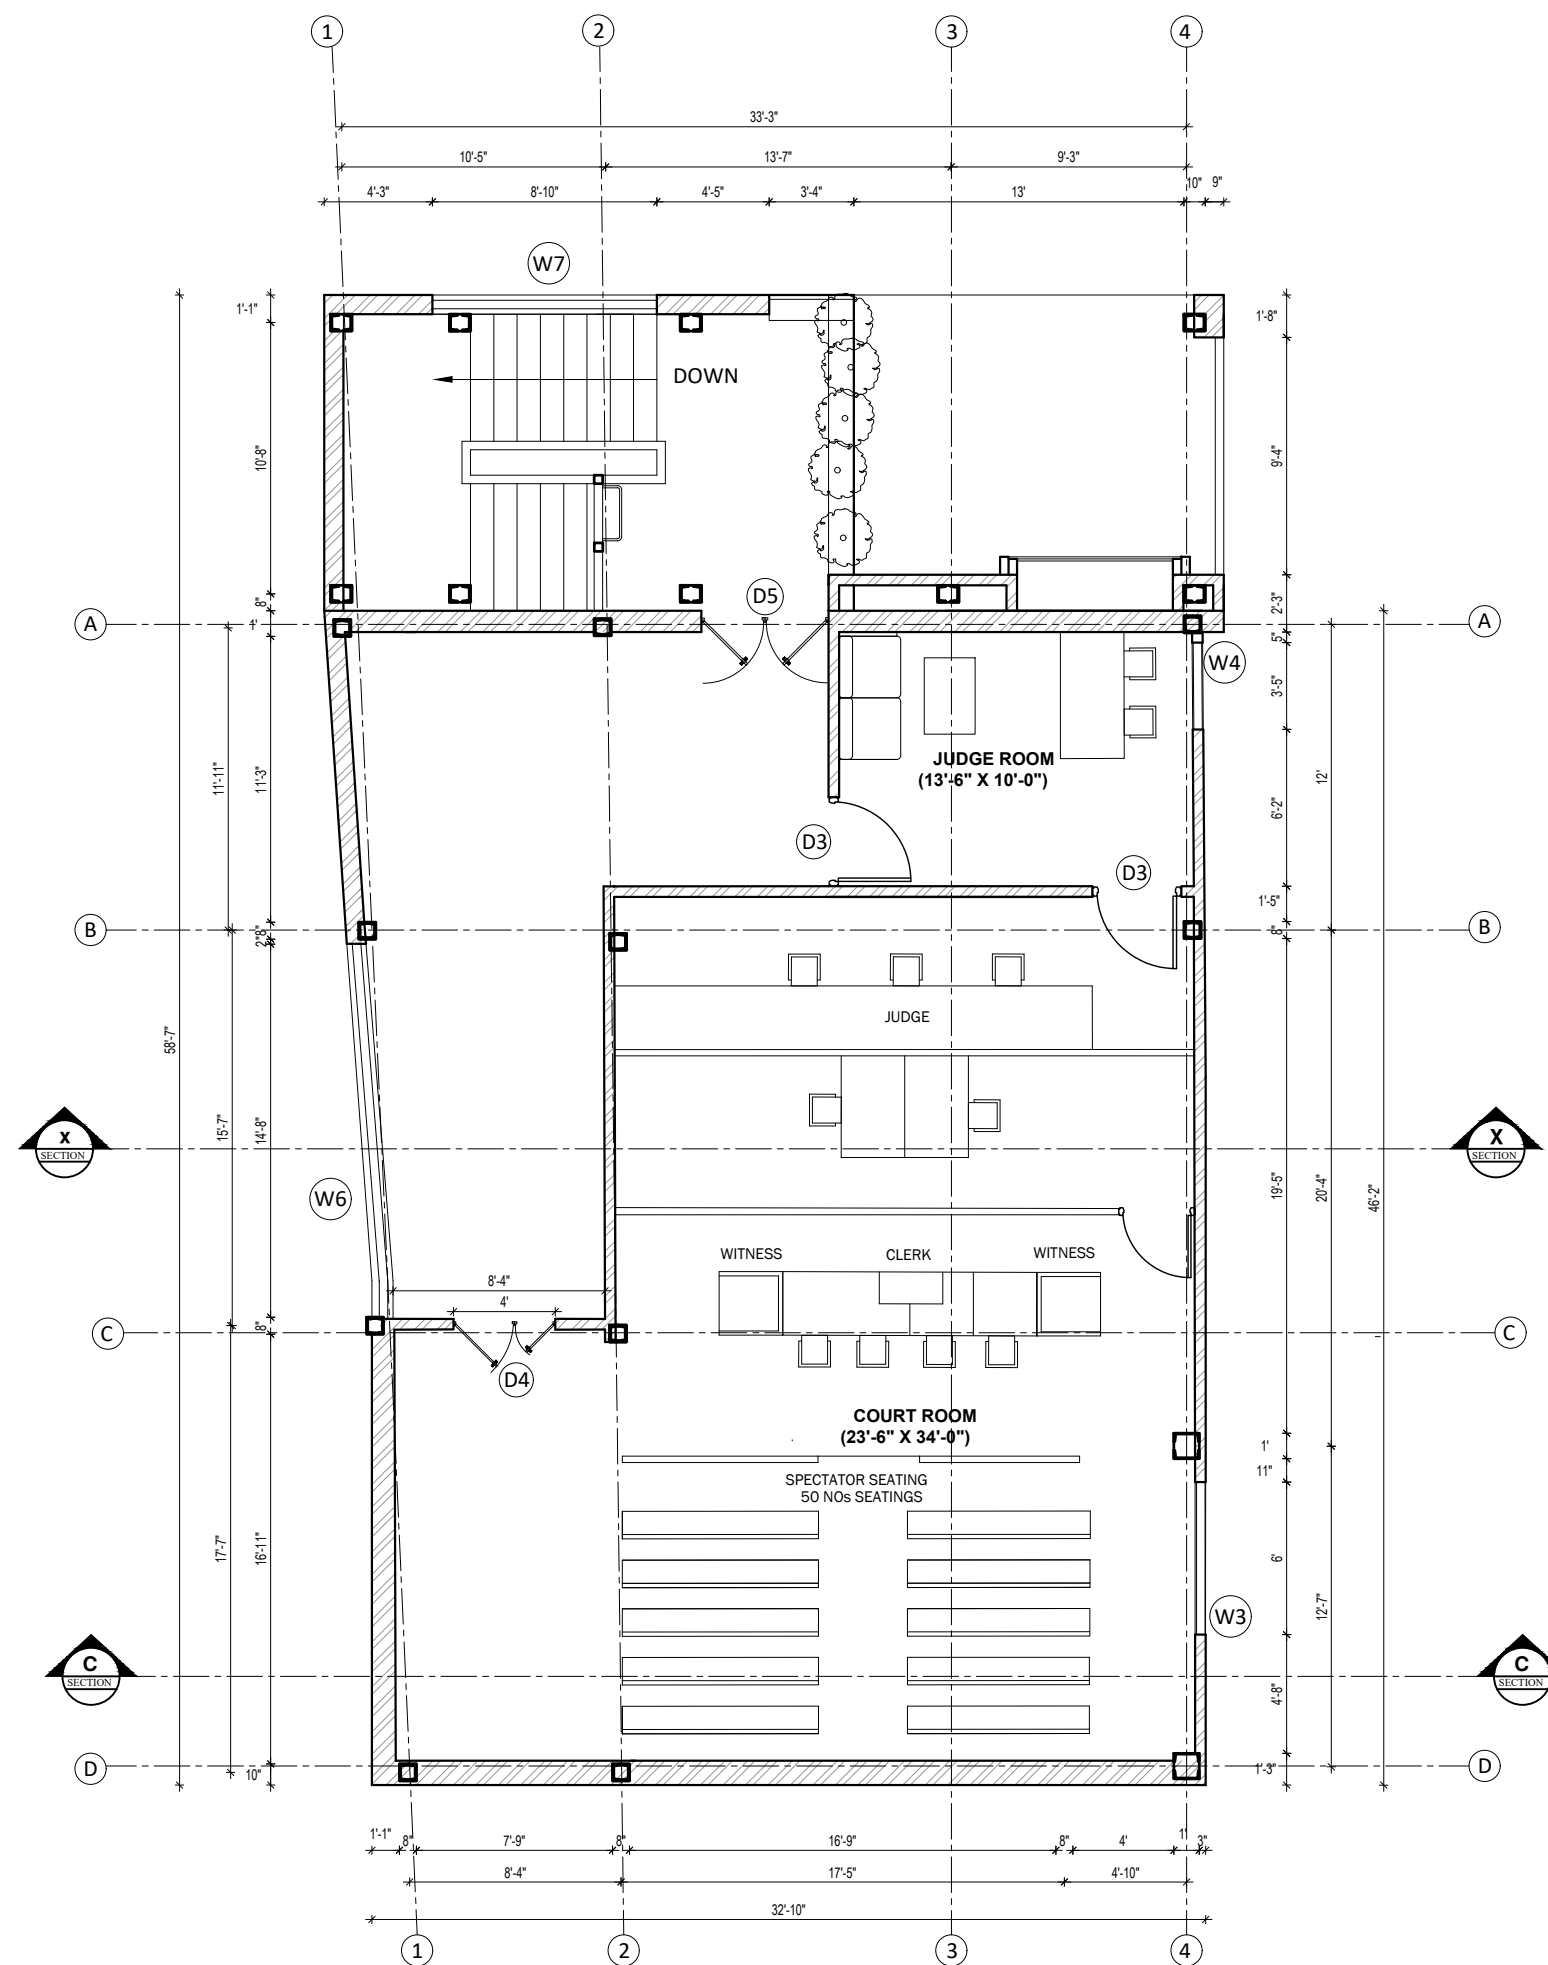

TOP FLOOR PLAN
AREA: 1975.02 SQ. FT.

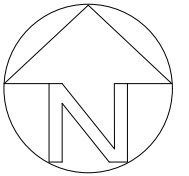

1. Do not scale drawings.
2. All dimensions are in millimeters unless noted otherwise.
3. Dimensions do not include finishes thickness (if otherwise mentioned).
4. All dimensions shall be verified on site before proceeding with the work.
5. LWA shall be notified in writing of any discrepancies.
6. Any areas in the sheet are approximate and indicative only.

[illegible]

CLIENT: GLOBAL COLLEGE
OF TECHNOLOGY

CLIENT:

ARCHITECTURAL DRAWING
(MAIN BLOCK)

DATE:

SCALE:

DRAWN BY : Ar. Dikshant Man Baisyet


DESIGN BY : Ar. Sabin Maharjan

SHEET No.:A-06


PAGE No.: 06



LINE WORK ARCHITECTS

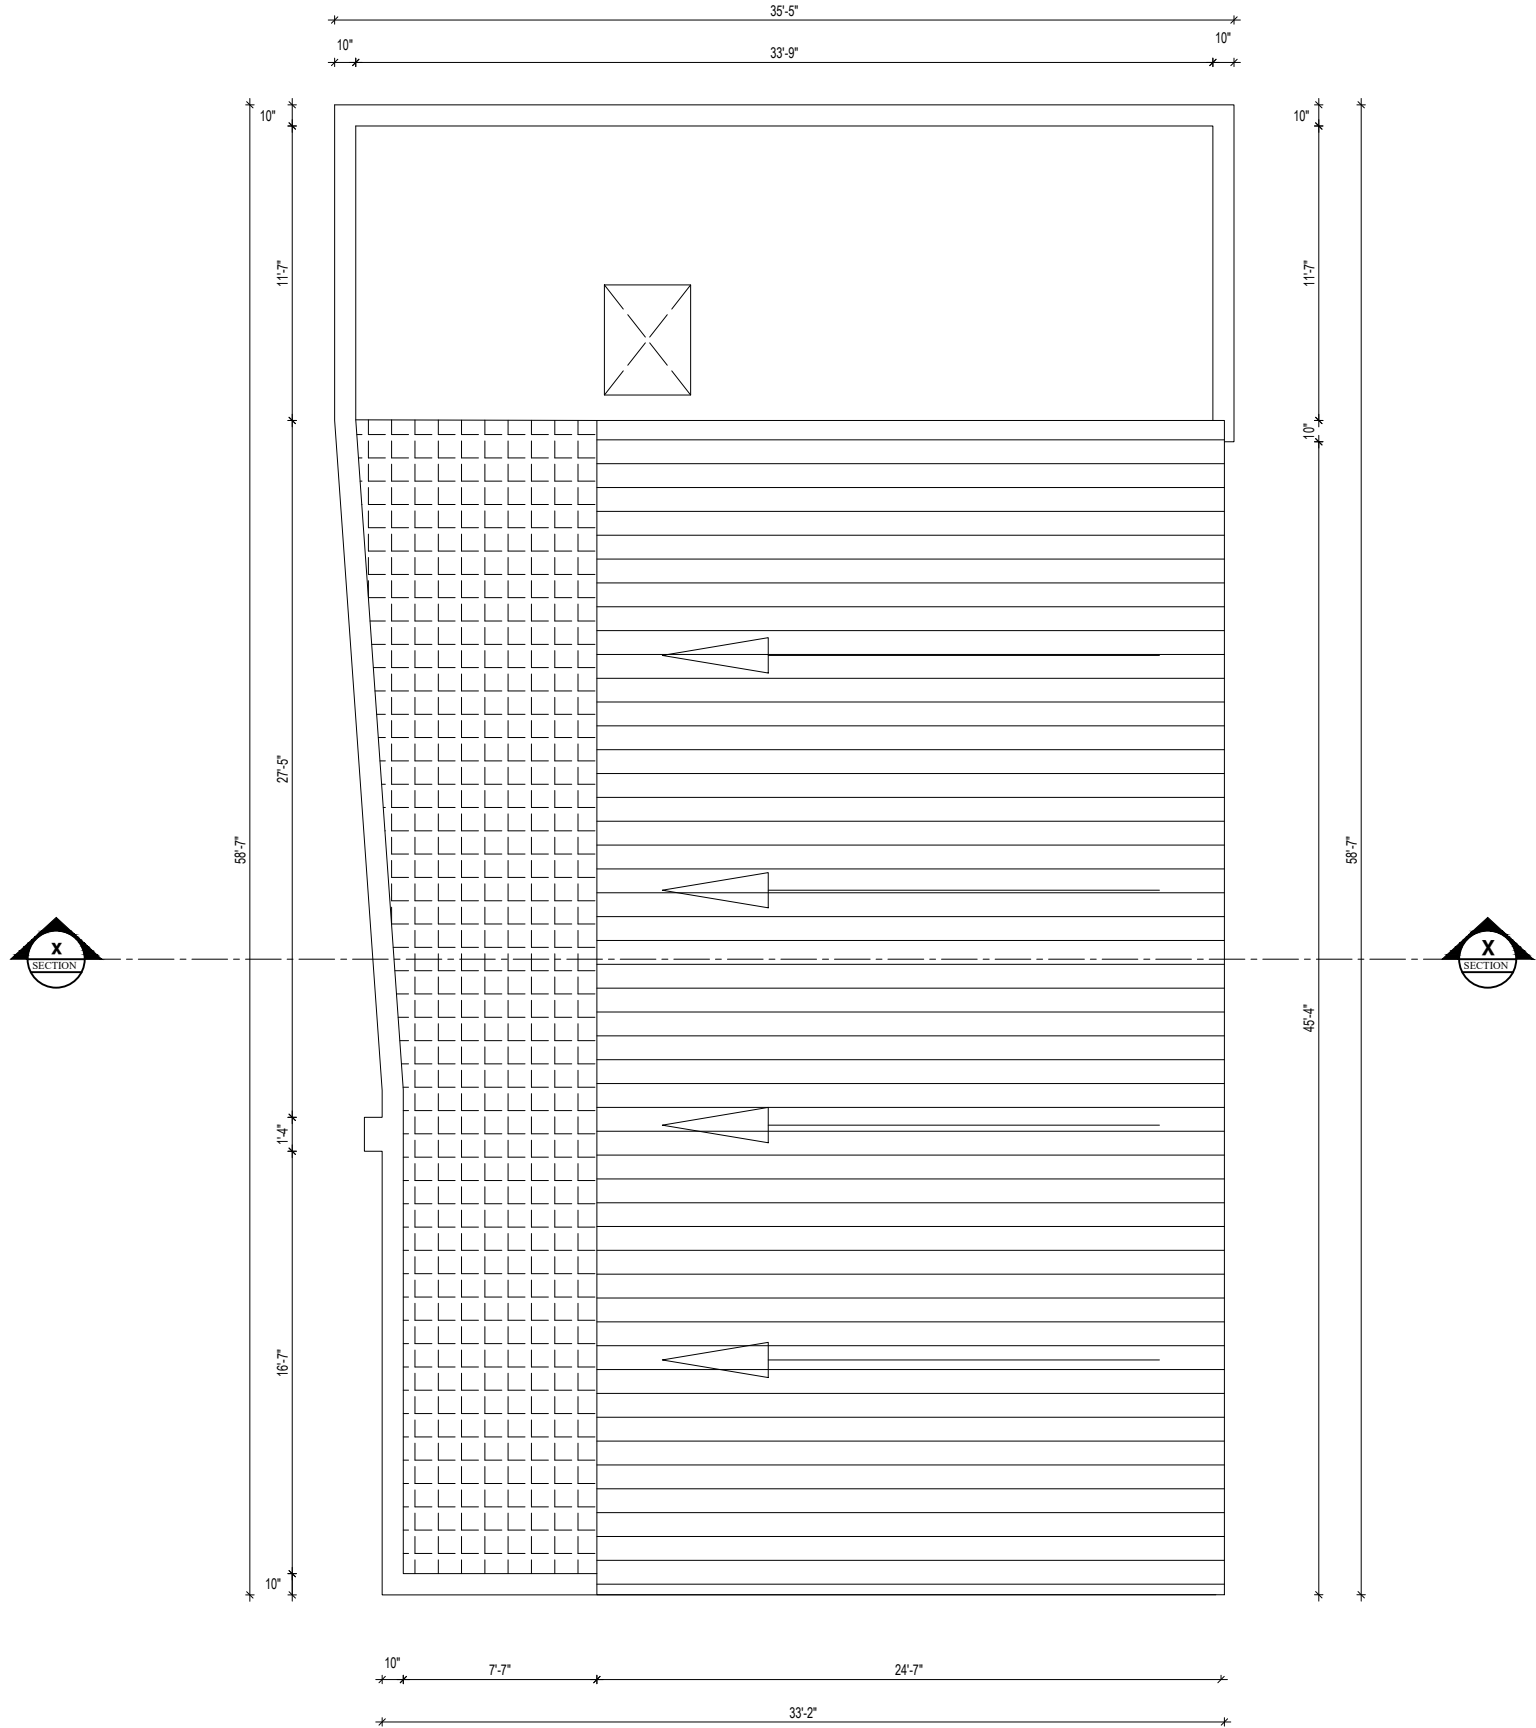

ROOF PLAN

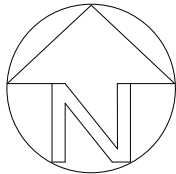

- 1. Do not scale drawings.
- 2. All dimensions are in millimeters unless noted otherwise.
- 3. Dimensions do not include finishes thickness (If otherwise mentioned).
- 4. All dimensions shall be verified on site before proceeding with the work.
- 5. LWA shall be notified in writing of any discrepancies.
- 6. Any areas in the sheet are approximate and indicative only.

Reason of Issue	Checked

CLIENT:
GLOBAL COLLEGE
OF TECHNOLOGY

CLIENT:
ARCHITECTURAL DRAWING
(MAIN BLOCK)

DATE:

SCALE:


DRAWN BY : Ar. Dikshant Man Baisyet

DESIGN BY : Ar. Sabin Maharjan

SHEET No.: A-07

PAGE No.: 07

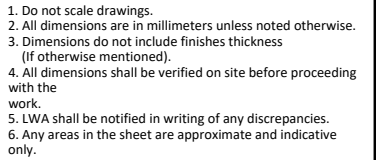

[illegible]

CLIENT: GLOBAL COLLEGE
OF TECHNOLOGY

CLIENT:

ARCHITECTURAL DRAWING
(MAIN BLOCK)

DATE: _____


SCALE:

DRAWN BY : Ar. Dikshant Man Baisyet


DESIGN BY : Ar. Sabin Maharjan

SHEET No.: A-08

PAGE No.: 08

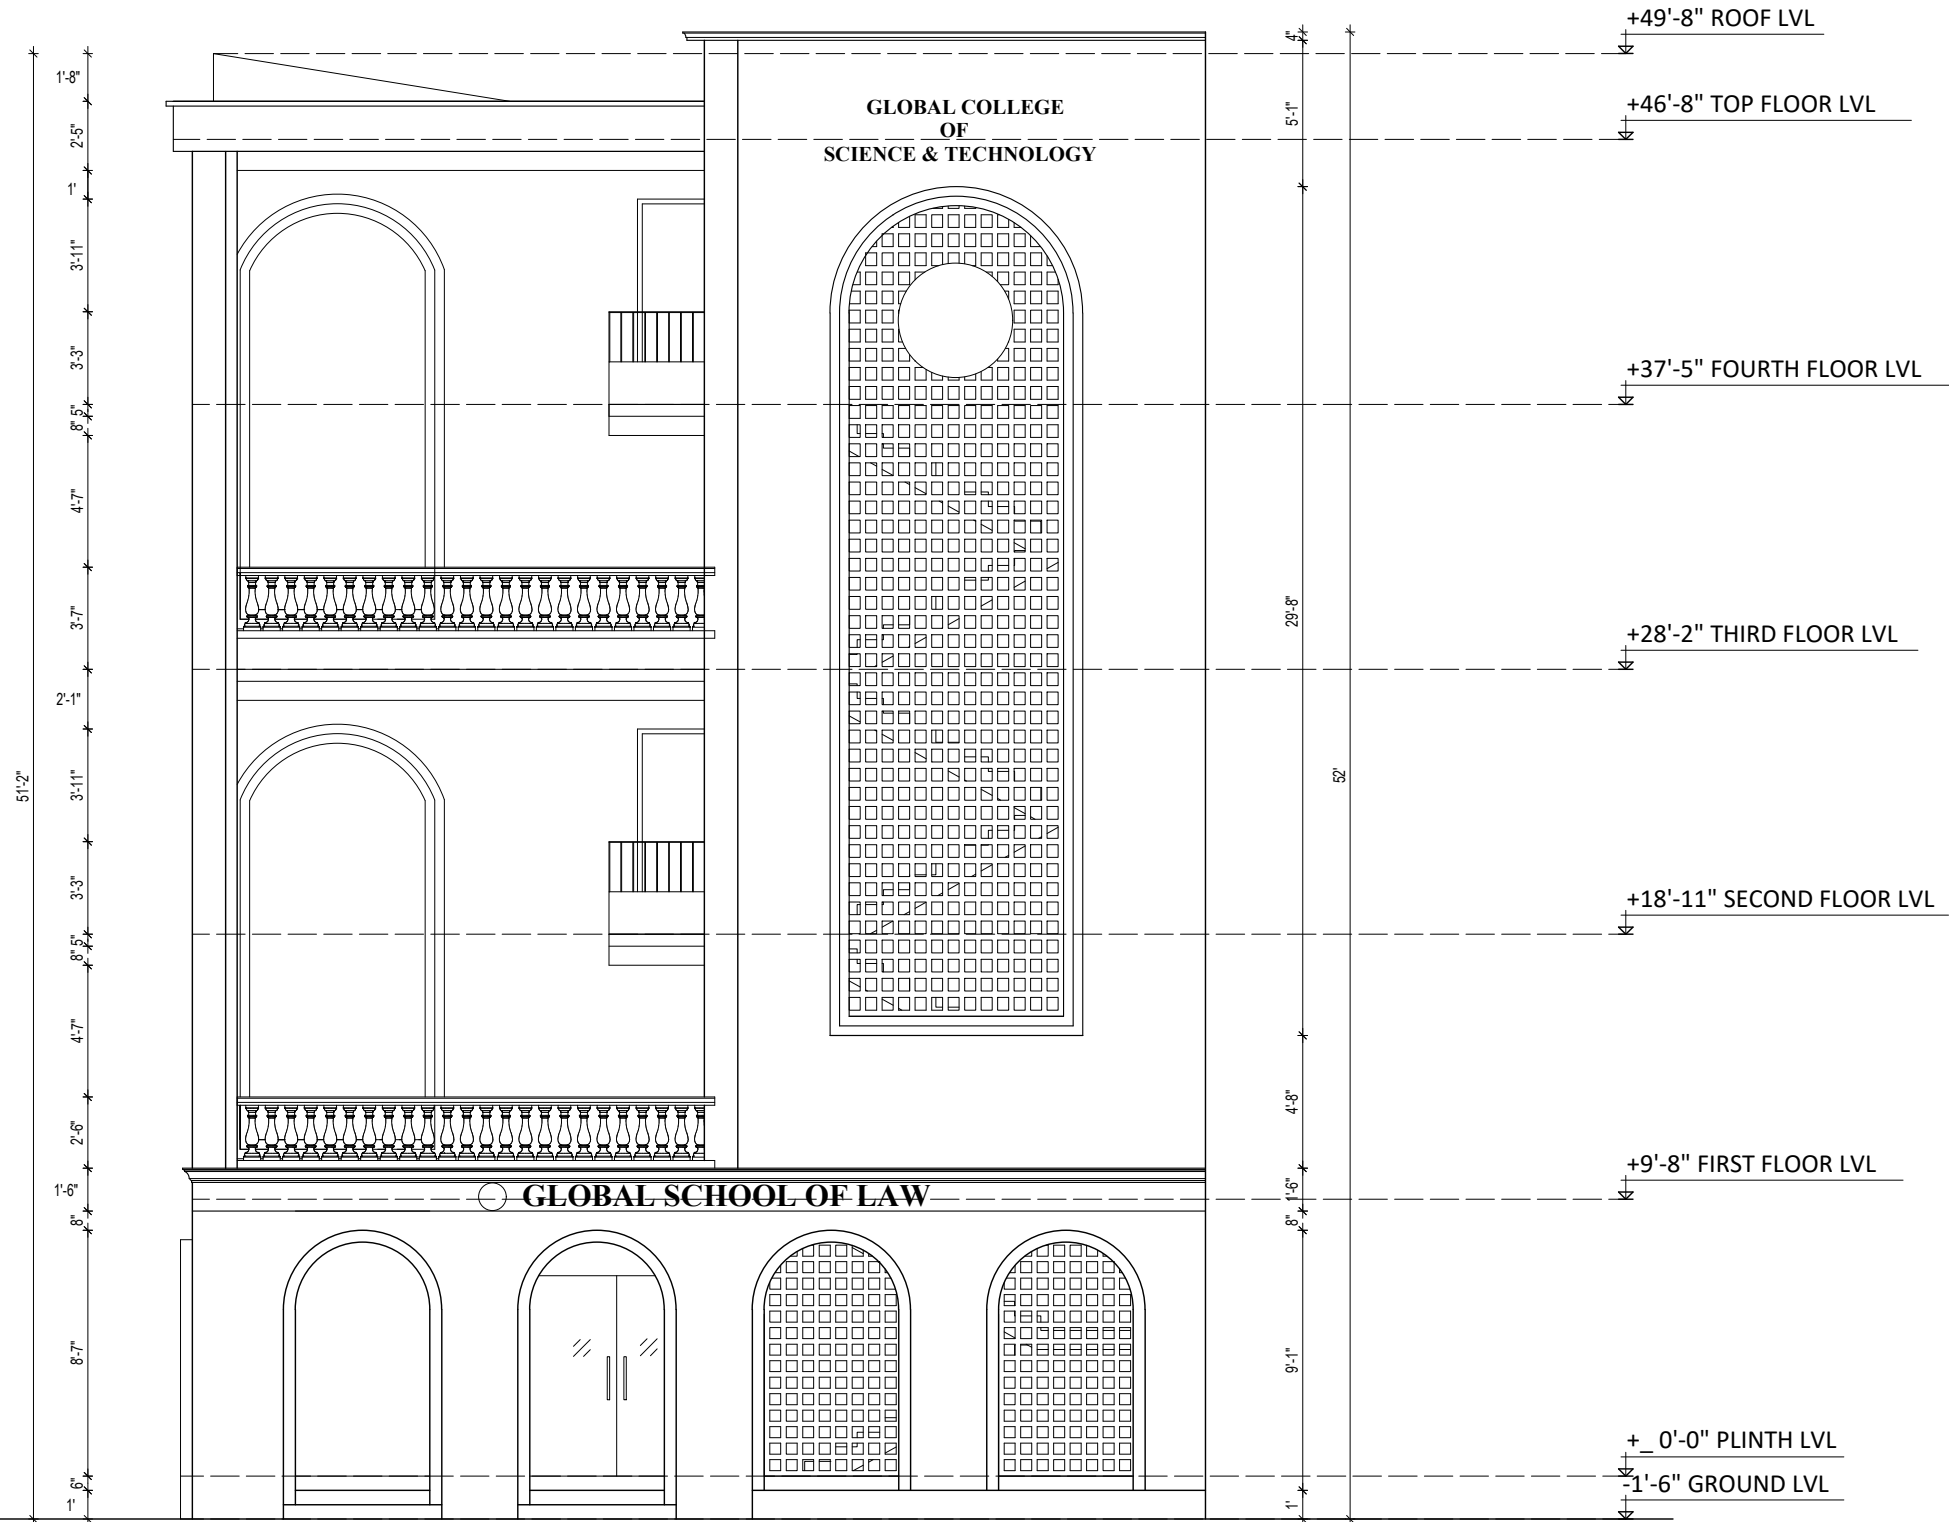

NORTH ELEVATION

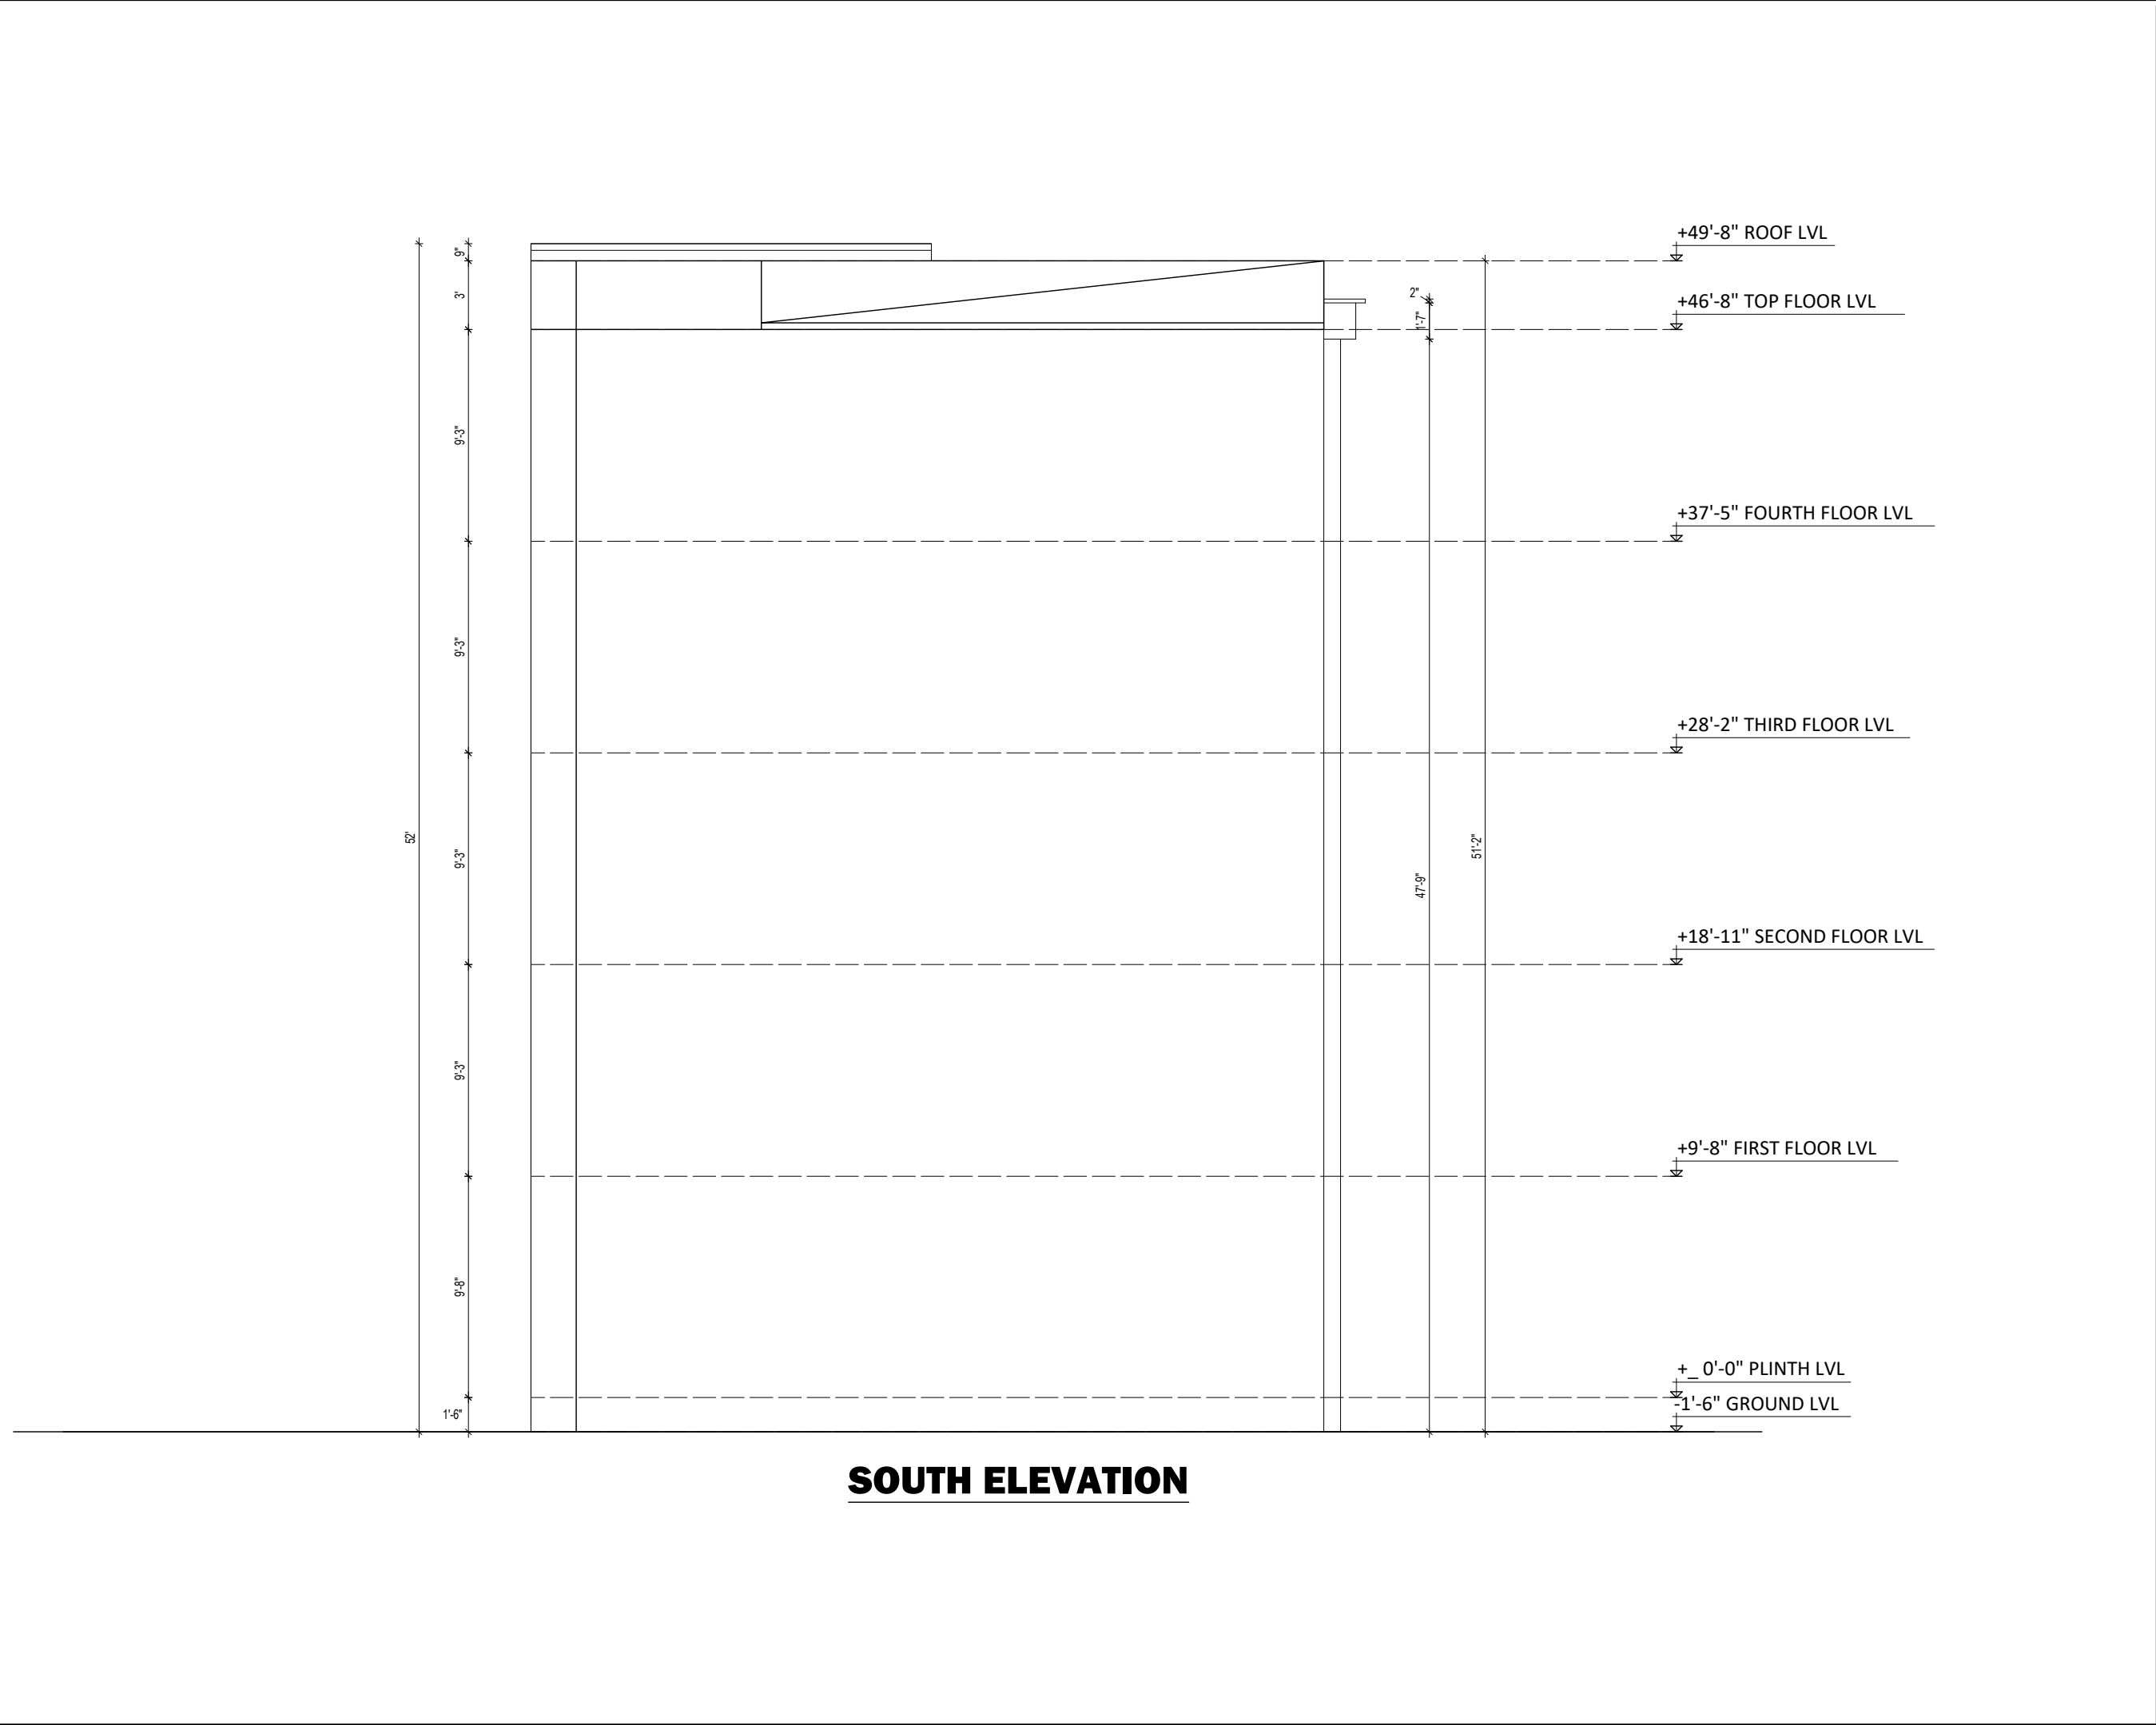

1. Do not scale drawings.
2. All dimensions are in millimeters unless noted otherwise.
3. Dimensions do not include finishes thickness (If otherwise mentioned).
4. All dimensions shall be verified on site before proceeding with the work.
5. LWA shall be notified in writing of any discrepancies.
6. Any areas in the sheet are approximate and indicative only.

Reason of Issue	Checked

CLIENT:
GLOBAL COLLEGE
OF TECHNOLOGY

CLIENT:
ARCHITECTURAL DRAWING
(MAIN BLOCK)

DATE:

SCALE:

DRAWN BY : Ar. Dikshant Man Baisyet


DESIGN BY : Ar. Sabin Maharjan

SHEET No.: A-09

PAGE No.: 09



LINE WORK ARCHITECTS

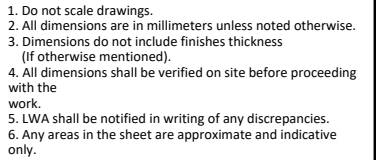[illegible]

CLIENT: GLOBAL COLLEGE
OF TECHNOLOGY

CLIENT:

ARCHITECTURAL DRAWING
(MAIN BLOCK)

DATE:


SCALE:

DRAWN BY : Ar. Dikshant Man Baisyet


DESIGN BY : Ar. Sabin Maharjan

SHEET No.:A-10

PAGE No.: 10

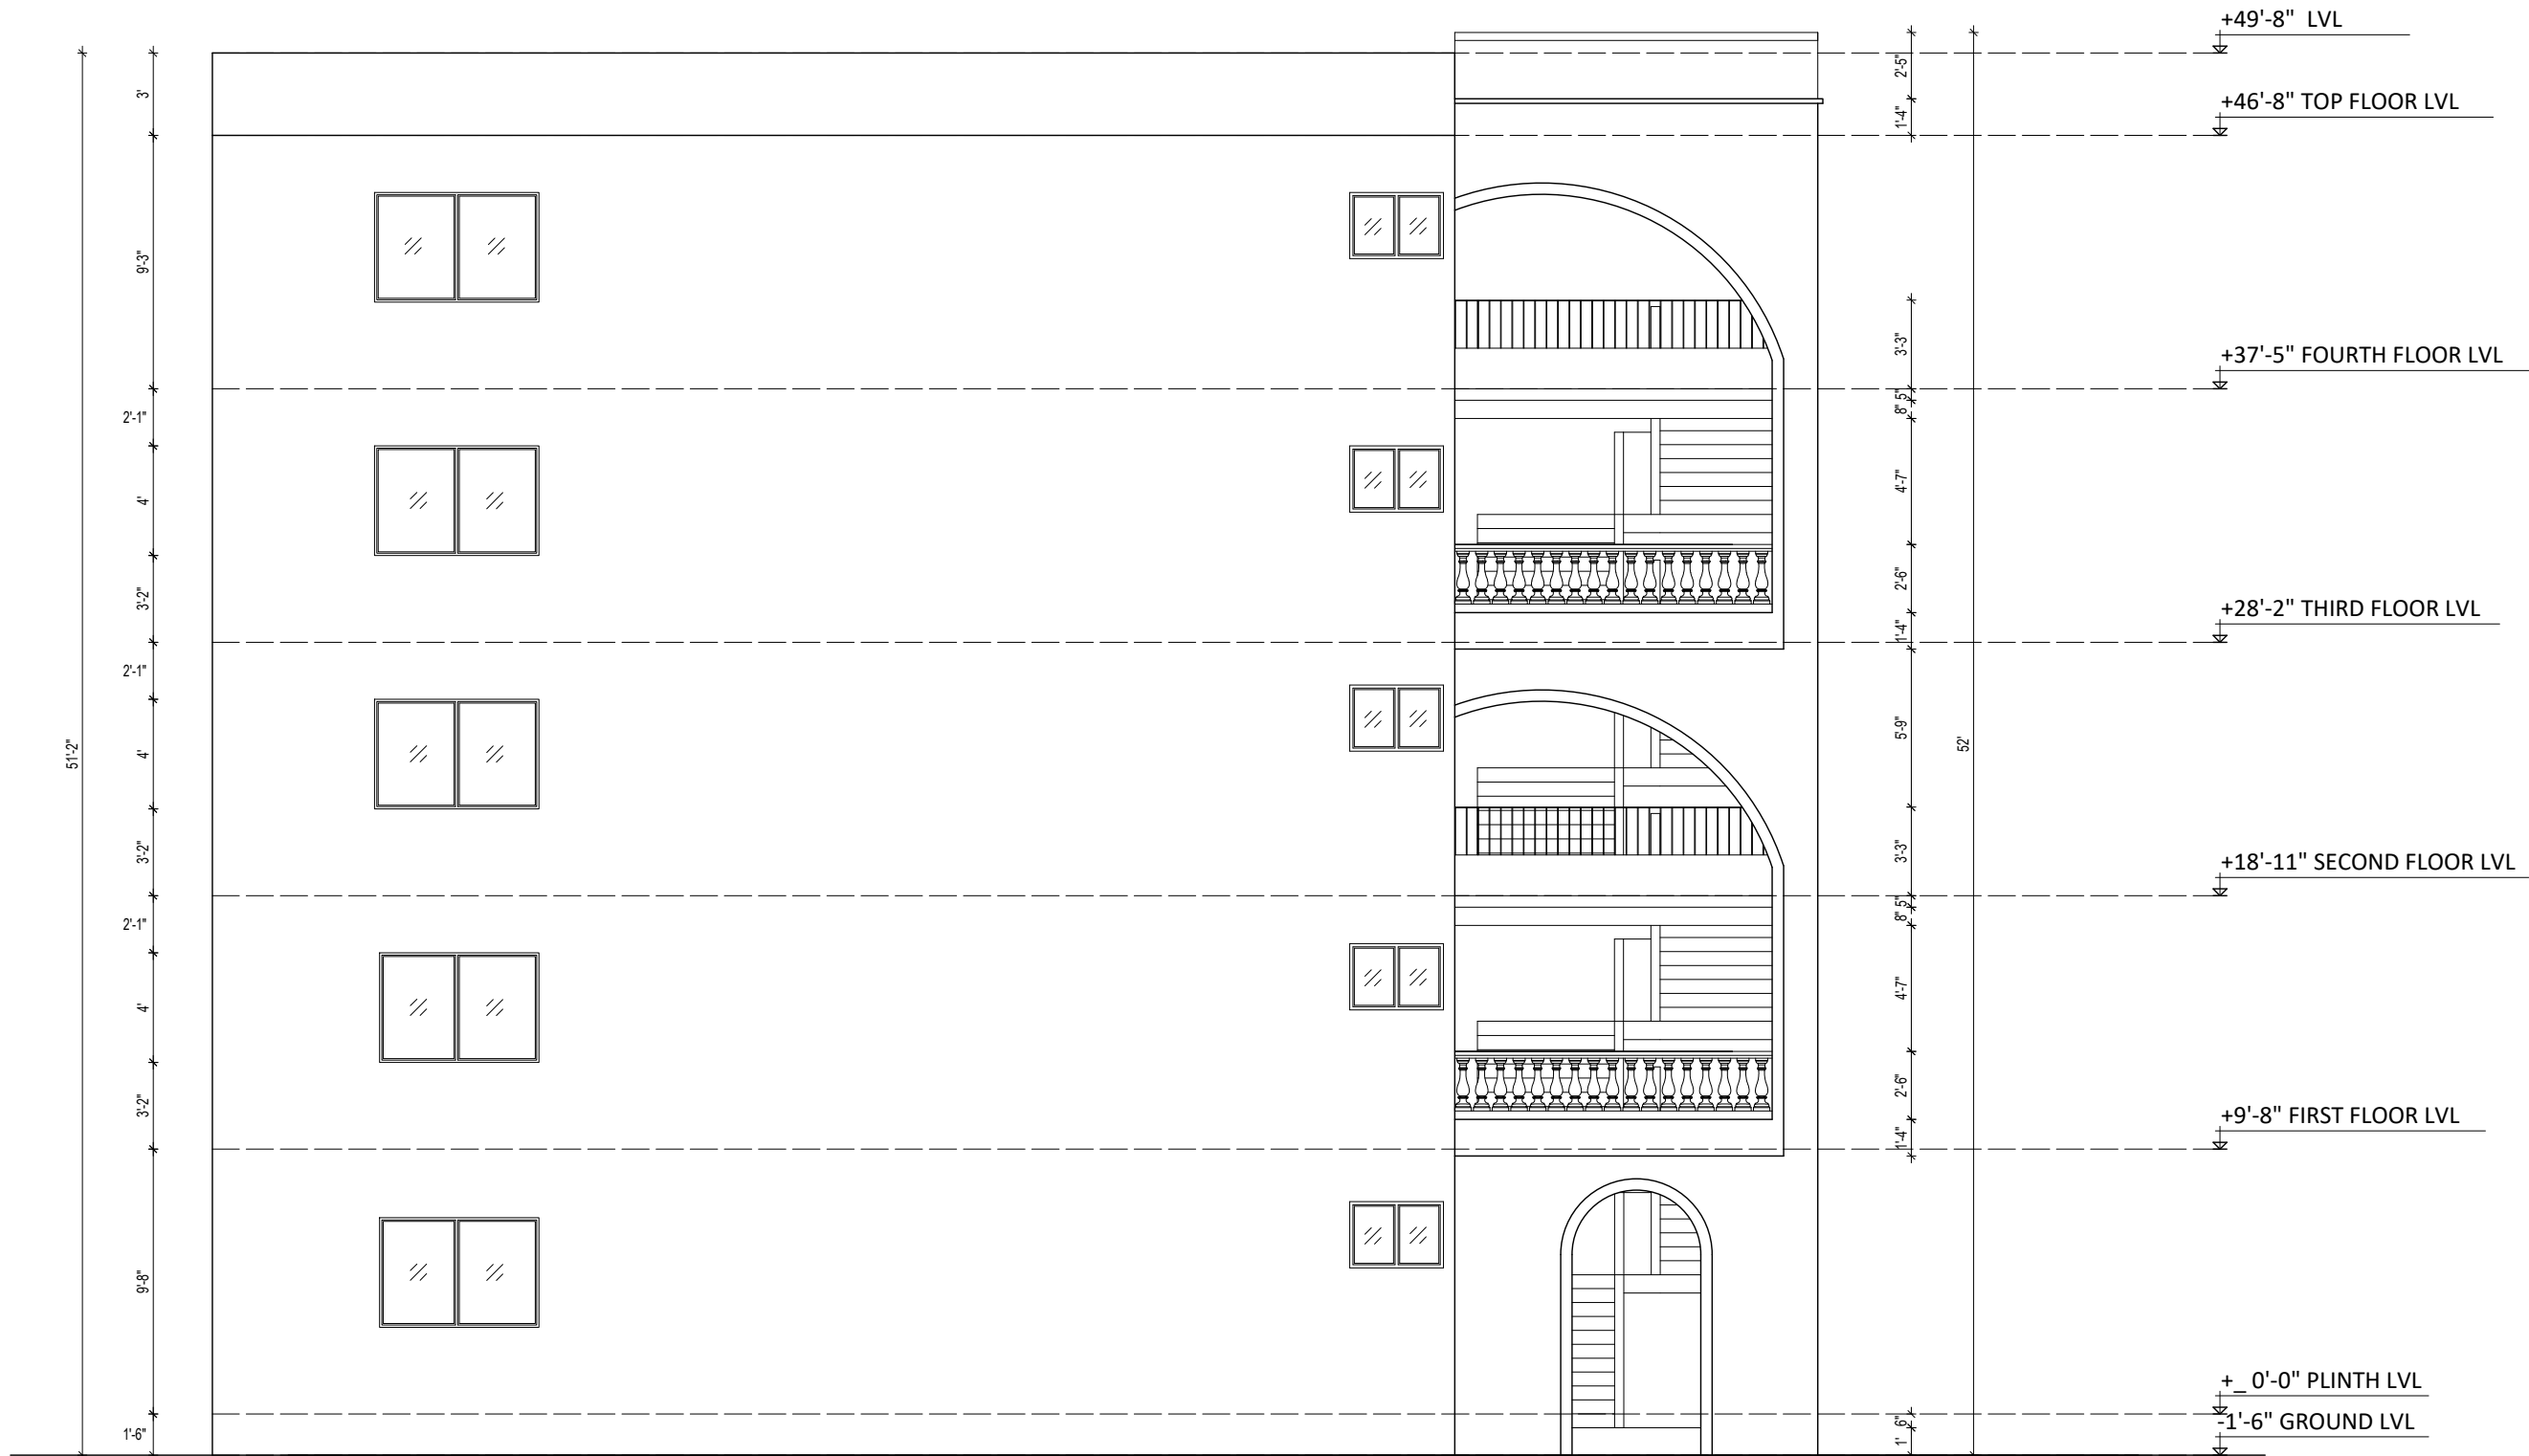

EAST ELEVATION

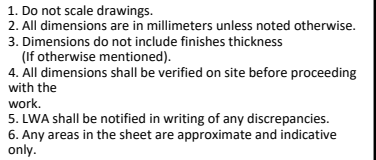[illegible]

CLIENT: GLOBAL COLLEGE
OF TECHNOLOGY

CLIENT:

ARCHITECTURAL DRAWING
(MAIN BLOCK)

DATE: _____


SCALE: _____

DRAWN BY : Ar. Dikshant Man Baisyet


DESIGN BY : Ar. Sabin Maharjan

SHEET No.:A-11

PAGE No.: 11

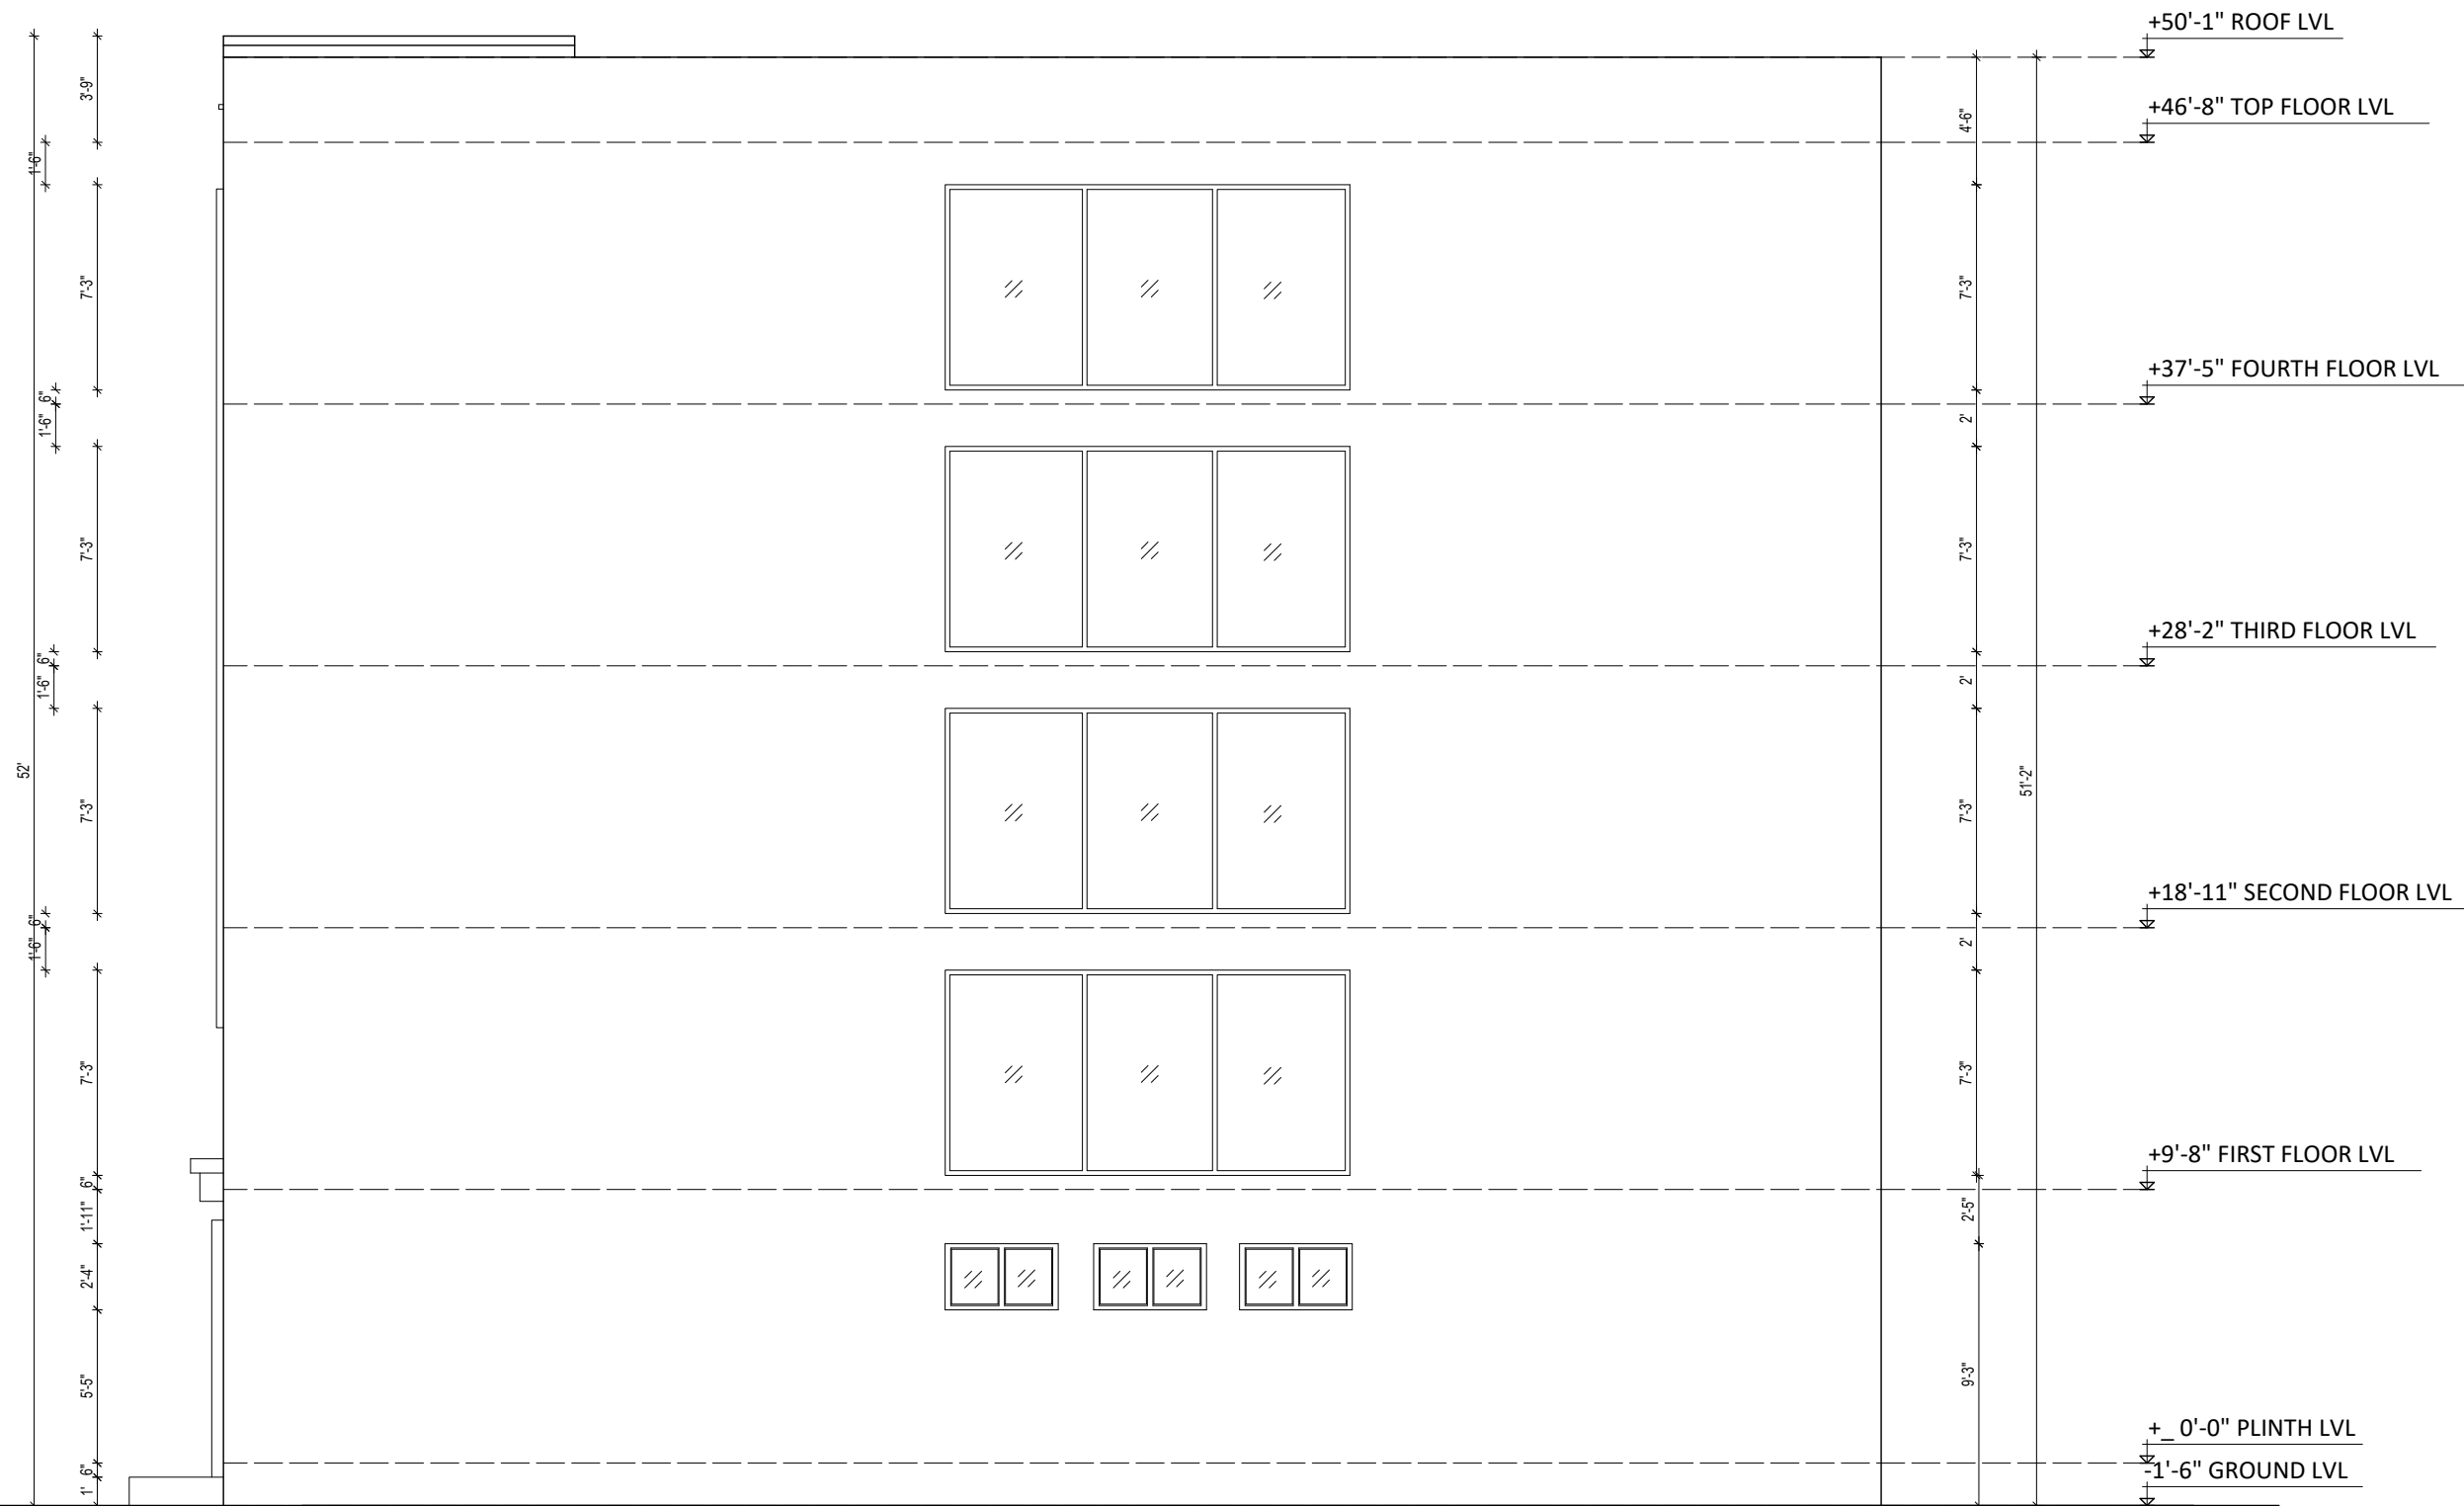

WEST ELEVATION

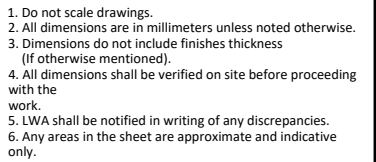[illegible]

CLIENT: GLOBAL COLLEGE
OF TECHNOLOGY

CLIENT:

ARCHITECTURAL DRAWING
(MAIN BLOCK)

DATE: _____

SCALE:


DRAWN BY : Ar. Dikshant Man Baisyet

DESIGN BY : Ar. Sabin Maharjan

SHEET No.: A-12

PAGE No.: 12



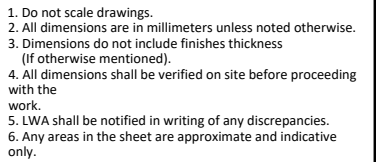

CLIENT: GLOBAL COLLEGE
OF TECHNOLOGY

CLIENT:

ARCHITECTURAL DRAWING
(MAIN BLOCK)

DATE: _____

SCALE: _____

DRAWN BY : Ar. Dikshant Man Baisyet


DESIGN BY : Ar. Sabin Maharjan

SHEET No.: A-13

PAGE No.: 13



GROUND FLOOR PLAN

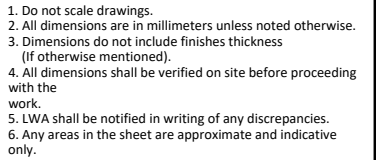[illegible]

CLIENT: GLOBAL COLLEGE
OF TECHNOLOGY

CLIENT:

ARCHITECTURAL DRAWING
(MAIN BLOCK)

DATE: _____


SCALE:

DRAWN BY : Ar. Dikshant Man Baisyet


DESIGN BY : Ar. Sabin Maharjan

SHEET No.: A-14

PAGE No.: 14

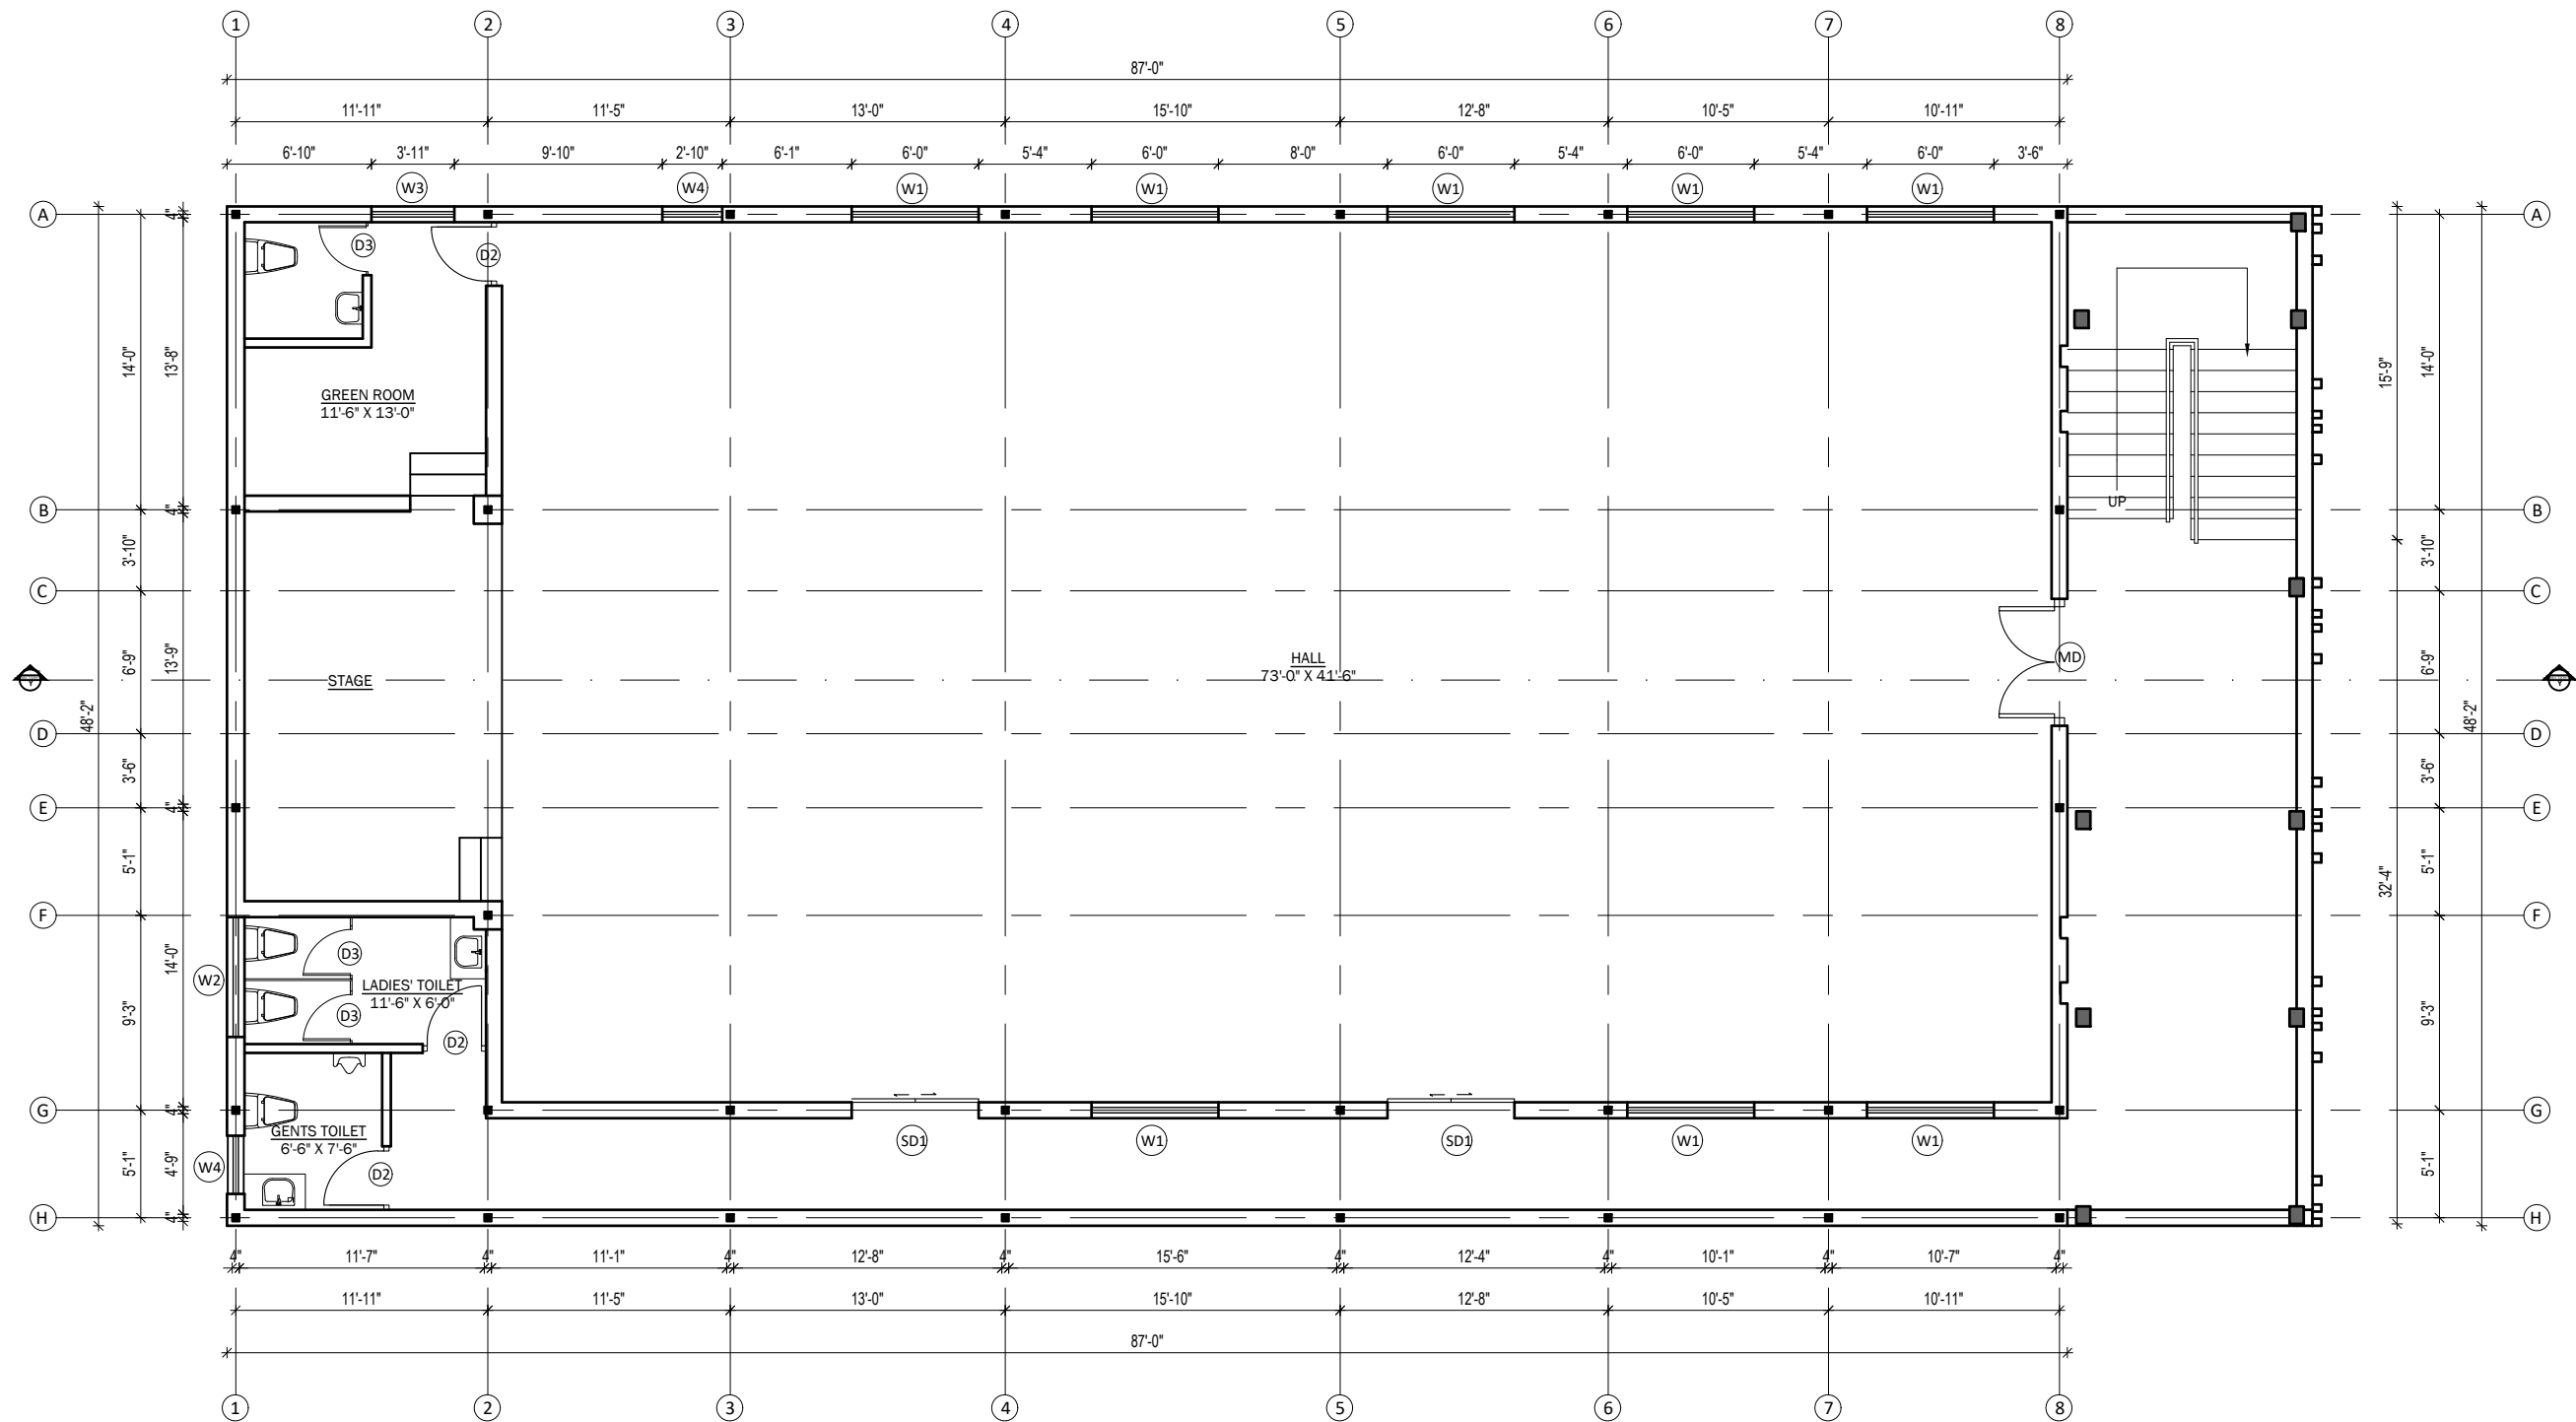

FIRST FLOOR PLAN

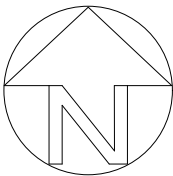

- 1. Do not scale drawings.
- 2. All dimensions are in millimeters unless noted otherwise.
- 3. Dimensions do not include finishes thickness (If otherwise mentioned).
- 4. All dimensions shall be verified on site before proceeding with the work.
- 5. LWA shall be notified in writing of any discrepancies.
- 6. Any areas in the sheet are approximate and indicative only.

Reason of Issue	Checked

CLIENT:
GLOBAL COLLEGE
OF TECHNOLOGY

CLIENT:
ARCHITECTURAL DRAWING
(MAIN BLOCK)

DATE:

SCALE:

DRAWN BY : Ar. Dikshant Man Baisyet


DESIGN BY : Ar. Sabin Maharjan

SHEET No.: A-15


PAGE No.: 15



LINE WORK ARCHITECTS

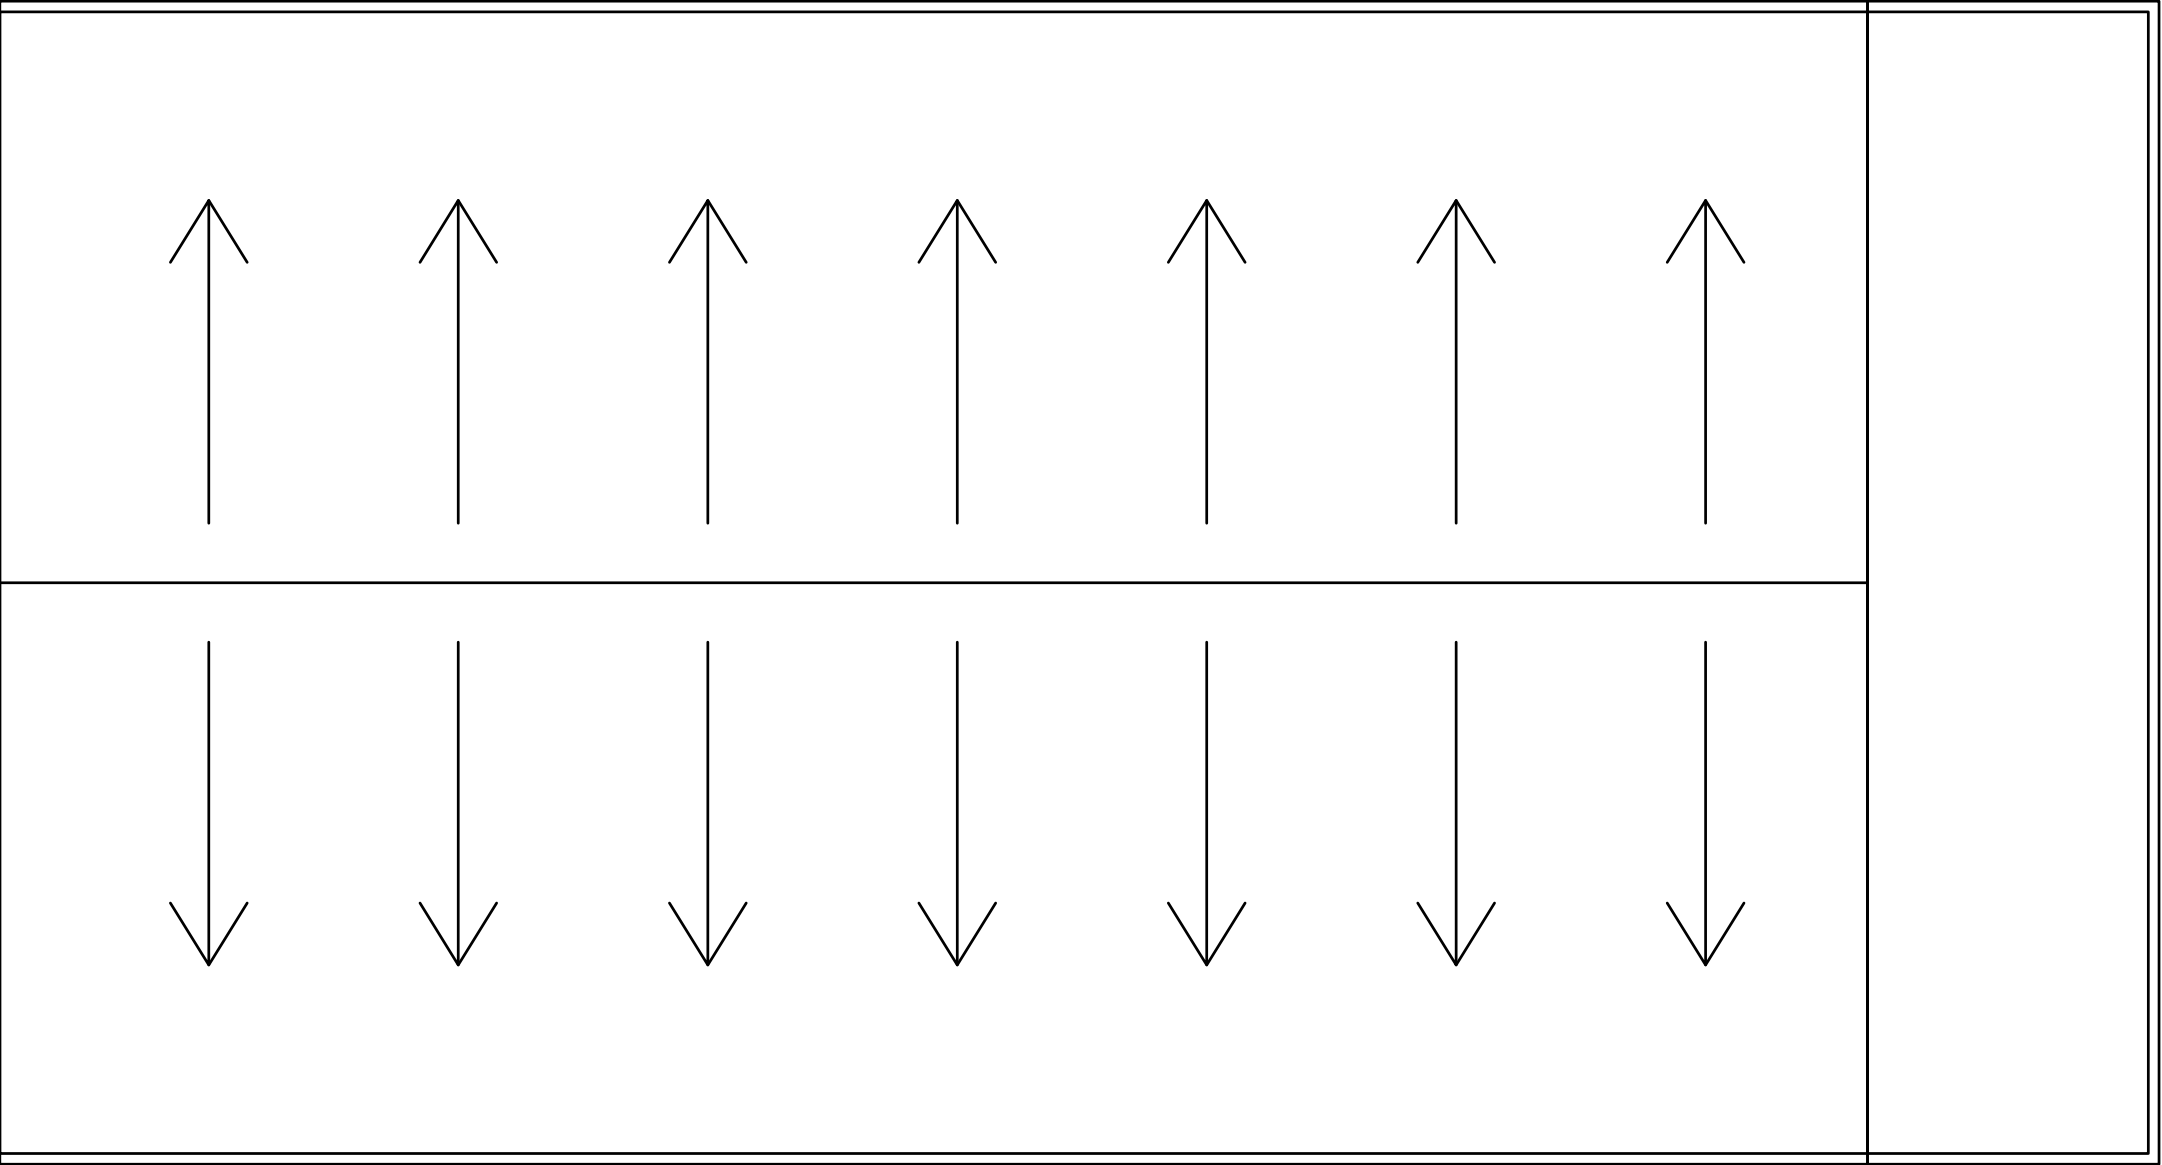

ROOF PLAN

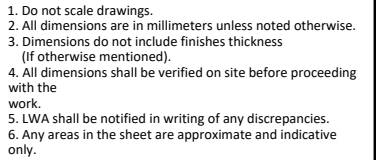


CLIENT: GLOBAL COLLEGE
OF TECHNOLOGY

DATE: _____SCALE: _____DRAWN BY : Ar. Dikshant Man Baisyet

DESIGN BY : Ar. Sabin Maharjan

SHEET No.: A-16PAGE No.: 16

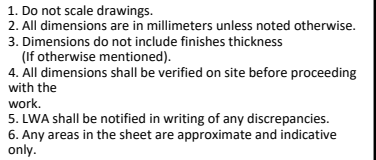[illegible]

CLIENT: GLOBAL COLLEGE
OF TECHNOLOGY

CLIENT:

ARCHITECTURAL DRAWING
(MAIN BLOCK)

DATE: _____

SCALE: _____


DRAWN BY : Ar. Dikshant Man Baisyet

DESIGN BY : Ar. Sabin Maharjan

SHEET No.: A-17

PAGE No.: 17

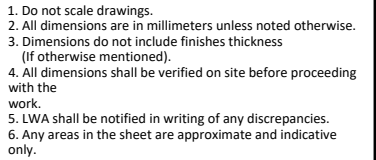

[illegible]

CLIENT: GLOBAL COLLEGE
OF TECHNOLOGY

CLIENT:

ARCHITECTURAL DRAWING
(MAIN BLOCK)

DATE:

SCALE:

DRAWN BY : Ar. Dikshant Man Baisyet

DESIGN BY : Ar. Sabin Maharjan

SHEET No.:A-18

PAGE No.: 18















